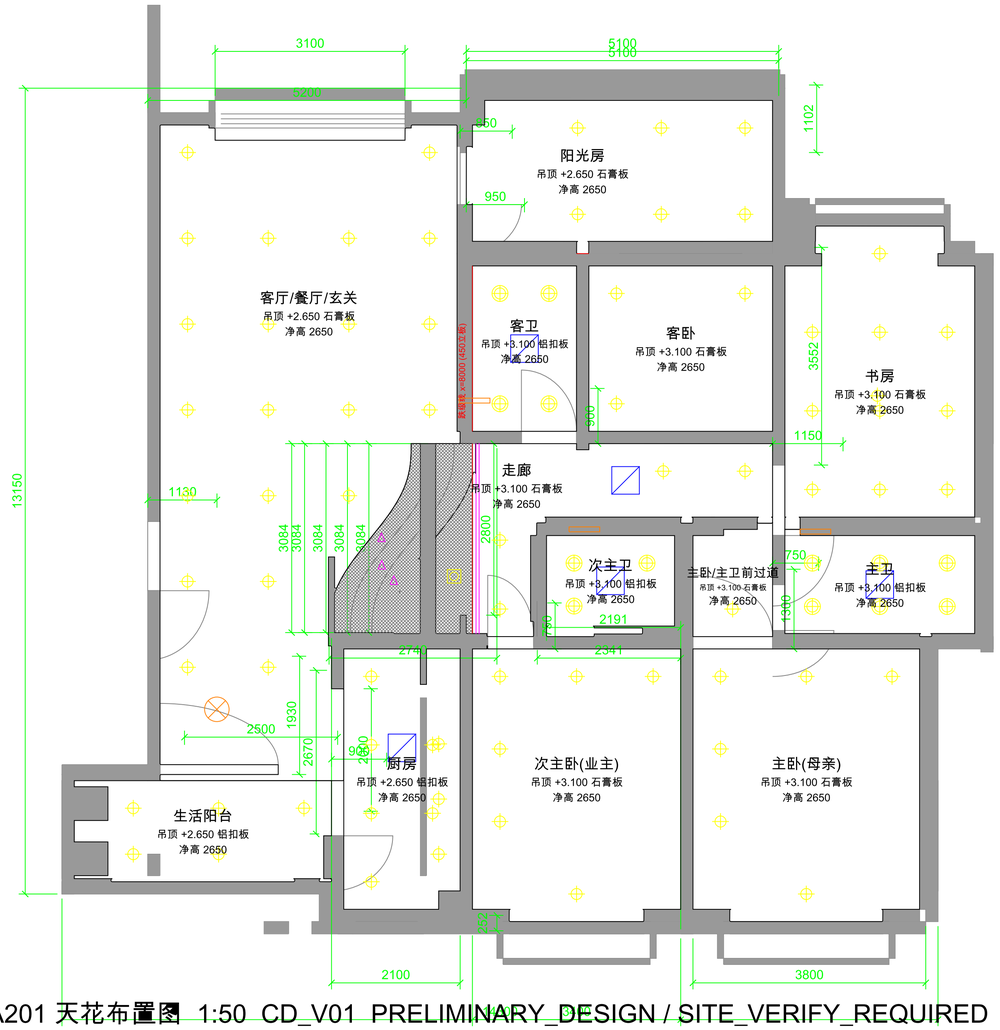



A201 天花布置图 1:50 CD_V01 PRELIMINARY_DESIGN / SITE_VERIFY_REQUIRED

A201 天花布置说明 (CD_V01 初步设计)

1. 原顶: 下区 +2.800, 上区 +3.250; 吊顶统一下返 150
2. 完成面: 下区 +2.650, 上区 +3.100; 两区净高 2650
3. 跌级: x=8000 (y4700-10900) + y=10900 东延至 x13100, 450 立板, 暗藏灯带 (P0.3.2)
4. 斜线区 = 上区地面(+0.450)位于下区原顶下, 净高 2350, 不吊顶, 明装灯 (4.31m²)
5. 卫生间/厨房/阳台 铝扣板, 其余 石膏板; 检修口 450x450 (阀门/接线处)
6. 灯具 94 个, 3000-4000K, 基础/任务/氛围分层; 坐标见 lighting_points.json/csv
7. 吊顶内管线空间、龙骨、梁位须现场核验 (SITE_VERIFY_REQUIRED); 150 下返不代表管线可全部安装
8. 楼梯区不吊顶; 逐踏步净高须现场复核
9. 与模型天花轮廓差异 2 处, CAD 按业主方案, 见 a201_ceiling_zones.json

图例

- 嵌入筒灯
- 防潮筒灯 IP44
- 明装射灯(原顶)
- 吊灯
- 镜前灯
- 踏步灯
- 跌级线 450 + 暗藏灯带
- 检修口 450x450

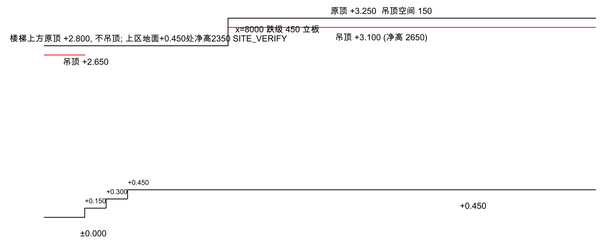

剖面示意 1-1 (y≈6000, 西→东), 1:50

A201 天花布置图

图号 A201　比例 1:50　图幅 A1　单位 mm

状态: 初步设计 PRELIMINARY_DESIGN - 非正式施工图, 尺寸须现场复核

源: A201_天花布置图.dxf sha256:6f58ca4337

出图: publish_dxf.py 2026-11-01