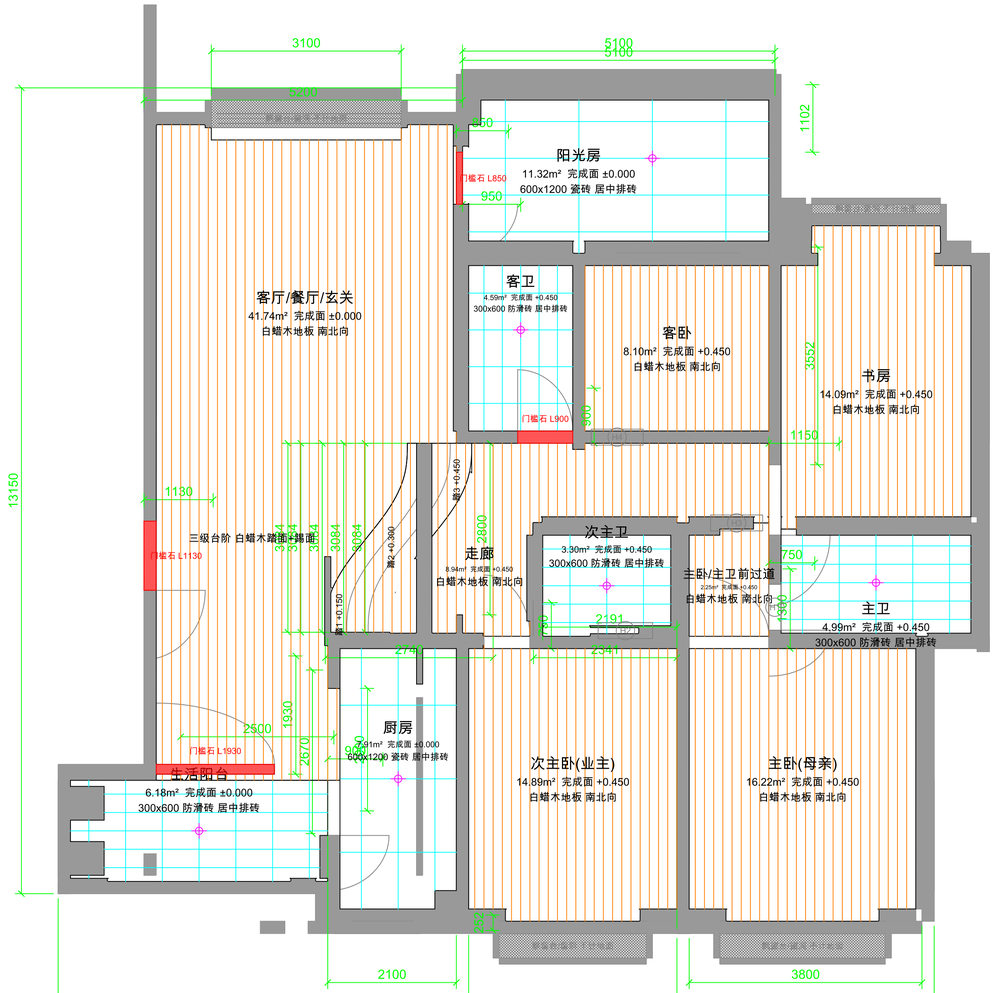


A202 地面铺装图 1:50 CD_V01 PRELIMINARY_DESIGN / SITE_VERIFY_REQUIRED

A202 地面铺装说明 (CD_V01 初步设计)

1. 木地板约 109.4m²: 白蜡木, 全屋统一南北向; 板宽按选品(图示线距150)
2. 瓷砖约 38.3m²: 厨房/阳光房 600x1200; 生活阳台/三卫 300x600 防滑砖 (规格 OWNER_REVIEW)
3. 排砖: 各间居中, 边砖 >= 1/3 砖, 起铺点见图; 损耗另计
4. 完成面: 下层 ±0.000, 上层 +0.450, 台阶 +0.150/+0.300/+0.450
5. 门槛石: 材质或标高变化处及客卫/次主卫门洞; 主卫(母亲遗老)门口不设凸起门槛
6. 卫生间找坡/地漏/挡水做法由业主排水方案定 -> HOLD
7. 分区来源: 模型 WHOLE_HOUSE_CORRECTED_SUPPORTED_V2 地面网格; 墙体: A103 V7 实测底图
8. 模型未覆盖的室内 2.25m² 按墙体围合补齐, 见 a202_gap_disposition.json
9. 品红框 = 模型有门但 A103 无洞口, 墙体按 A103 保留, 待确认
10. 面积为图面净面积, 下单以现场复尺为准 (SITE_VERIFY_REQUIRED)

图例

- 木地板
- 瓷砖分缝
- 门槛石
- 起铺点
- 待确认 (HOLD)
- 飘窗/窗洞, 不计地面

HOLD / 待确认 (图中品红圈)

H1 主卫(母亲遗老)门口: 不设凸起门槛; 排水/挡水做法待定
H2 模型有门(R3_SLIDING_LEAF), A103 无洞口: 墙按 A103 保留, 开洞待确认
H3 模型有门(V4_D-BATHM_LEAF_0), A103 无洞口: 墙按 A103 保留, 开洞待确认
H4 模型有门(V4_D-GUEST-ROOM_LEAF_0), A103 无洞口: 墙按 A103 保留, 开洞待确认

A202 地面铺装图

图号 A202 比例 1:50 图幅 A1 单位 mm
状态: 初步设计 PRELIMINARY_DESIGN - 非正式施工图, 尺寸须现场复核
源: A202_地面铺装图.dxf sha256:5c4490080e
出图: publish_dxf.py 2026-10-31