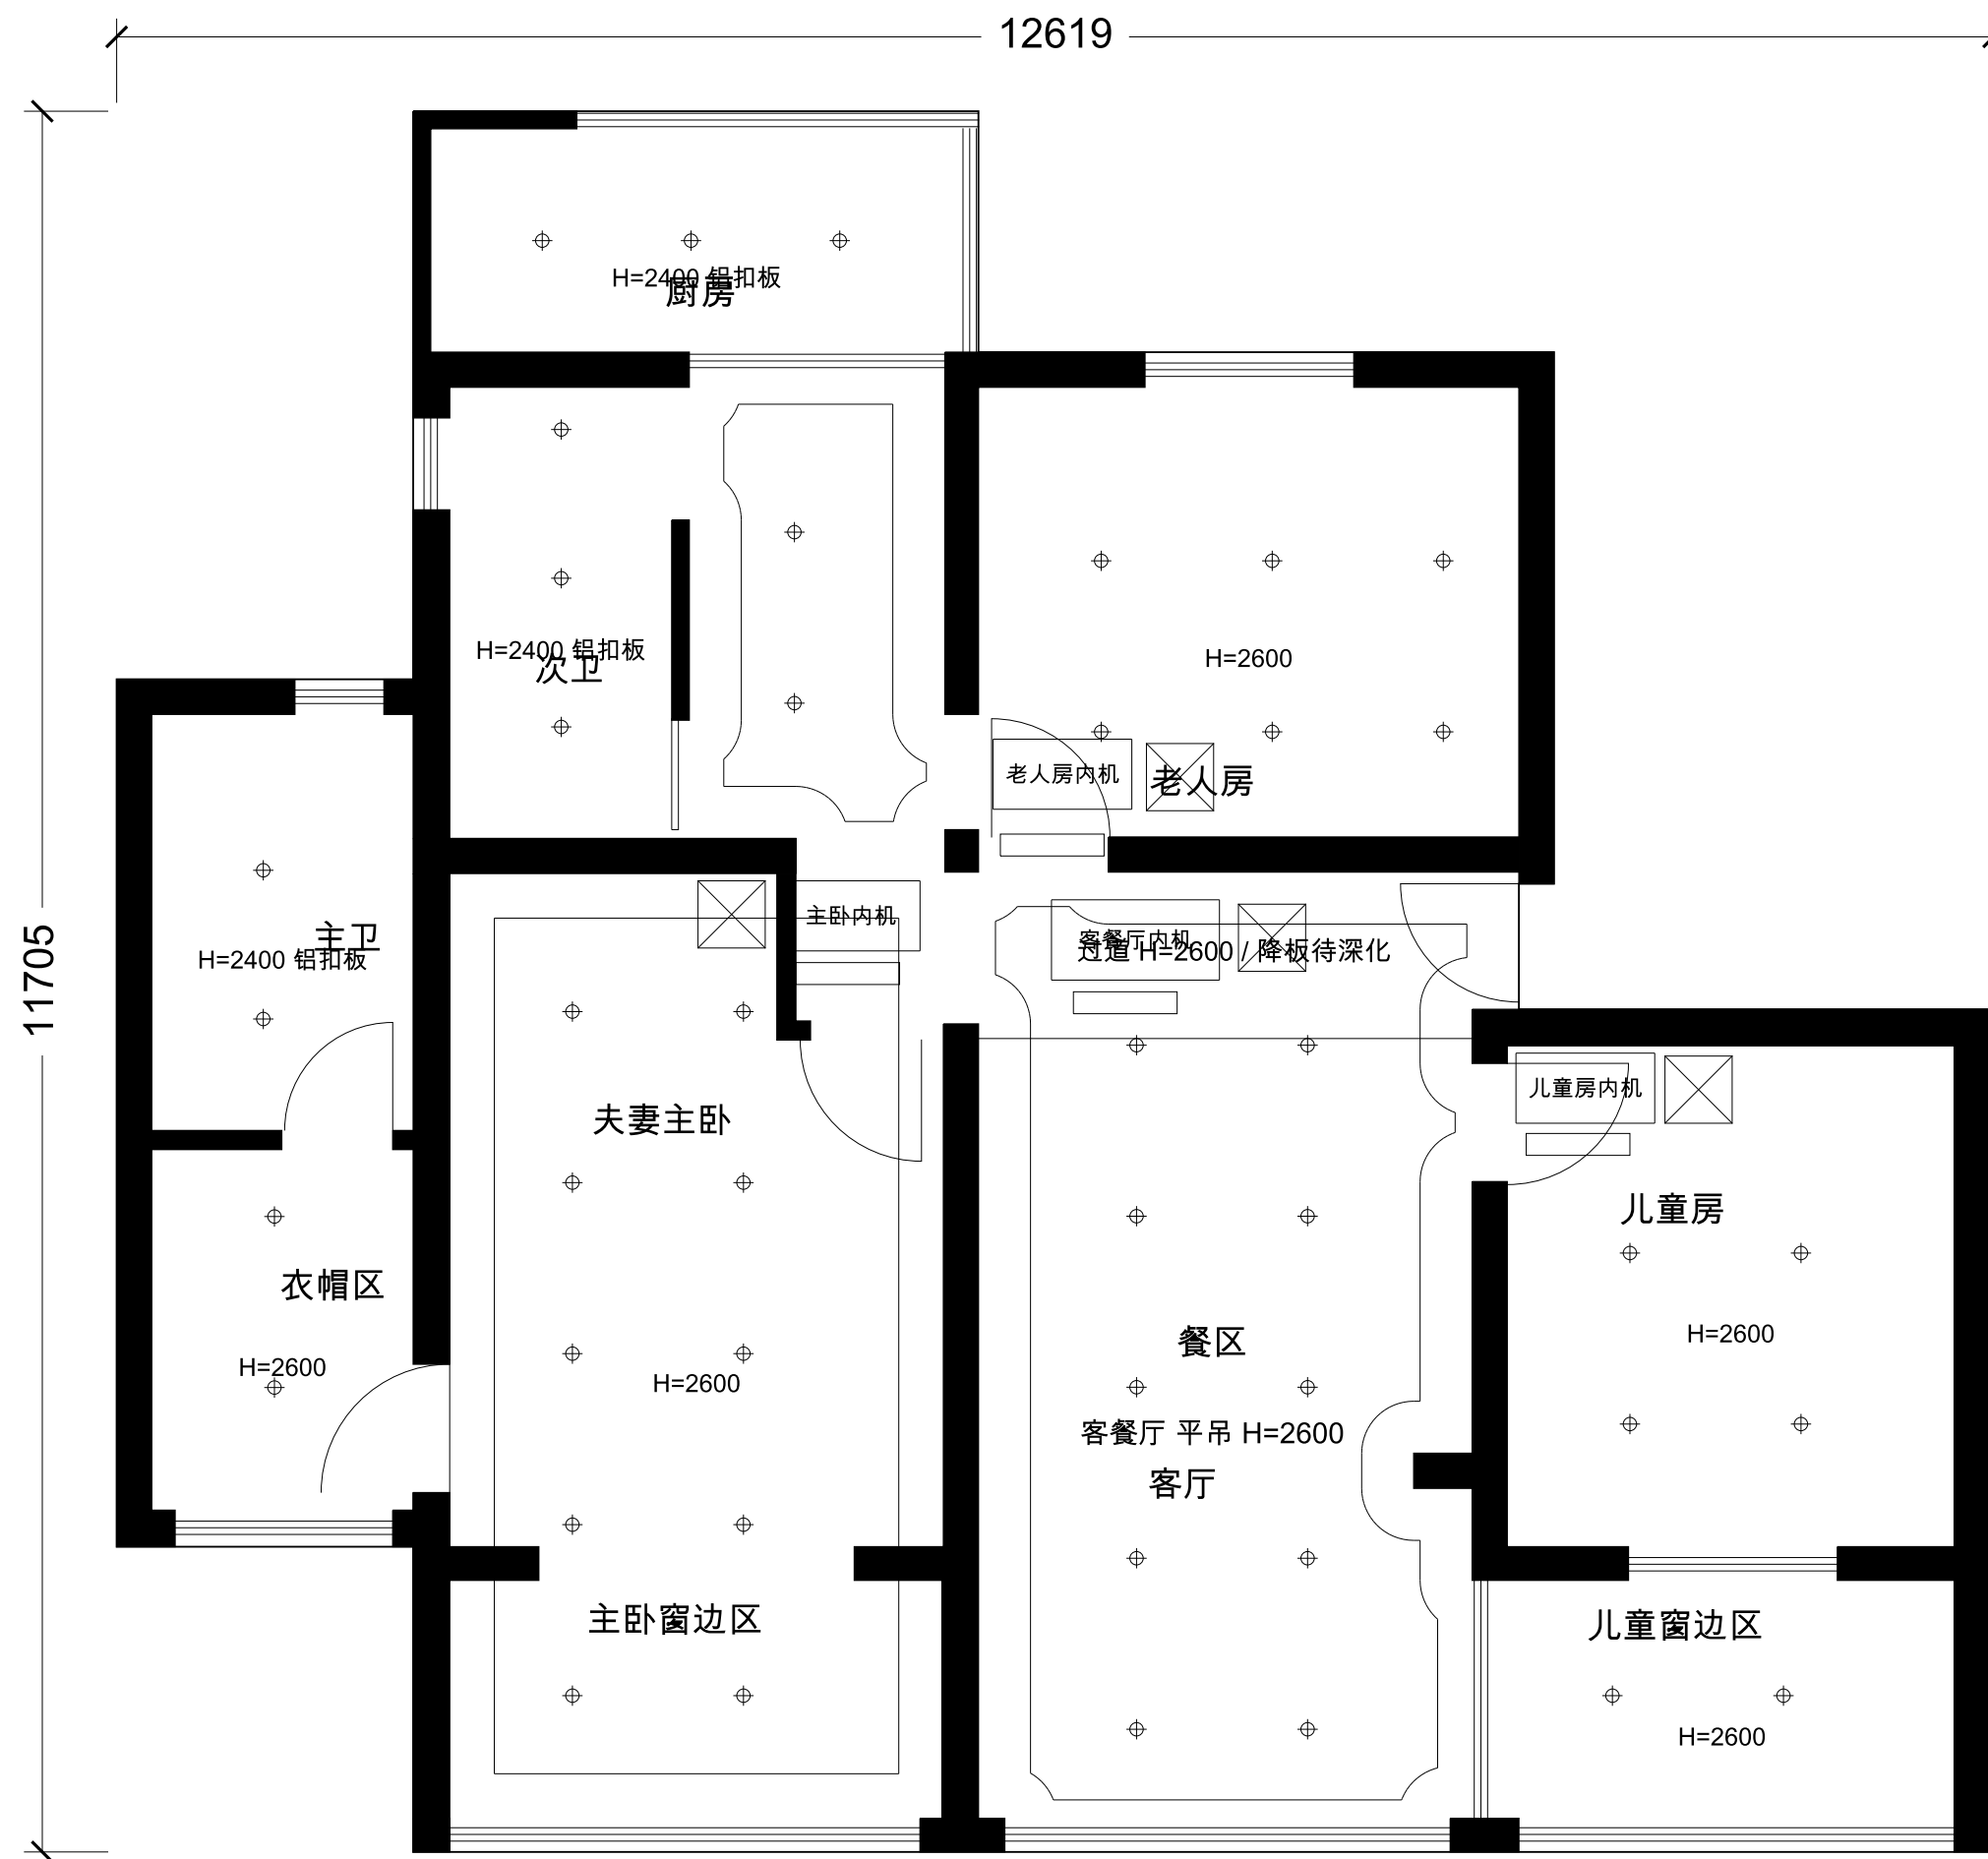


图纸说明 / NOTES

尺寸依据：A7 PNG × 9.82mm/px，非现场测量。

门表参考跨距#结构洞口；门套及设备SKU待确认。

干区吊顶2600 / 湿区2400 / 墙2700，现场复核。

· 图例：虚线框=风管式内机 (藏吊顶)；细实线框=送风口；☒=检修口450×450

· 多联机一拖多，外机1台机位待现场确认；内机品牌/型号待确认

· 筒灯 Ø90 (厨卫防雾型)，~1150mm网格，选型待确认

· 虚线=灯带/吊顶边界；层高基准以现场复尺为准