


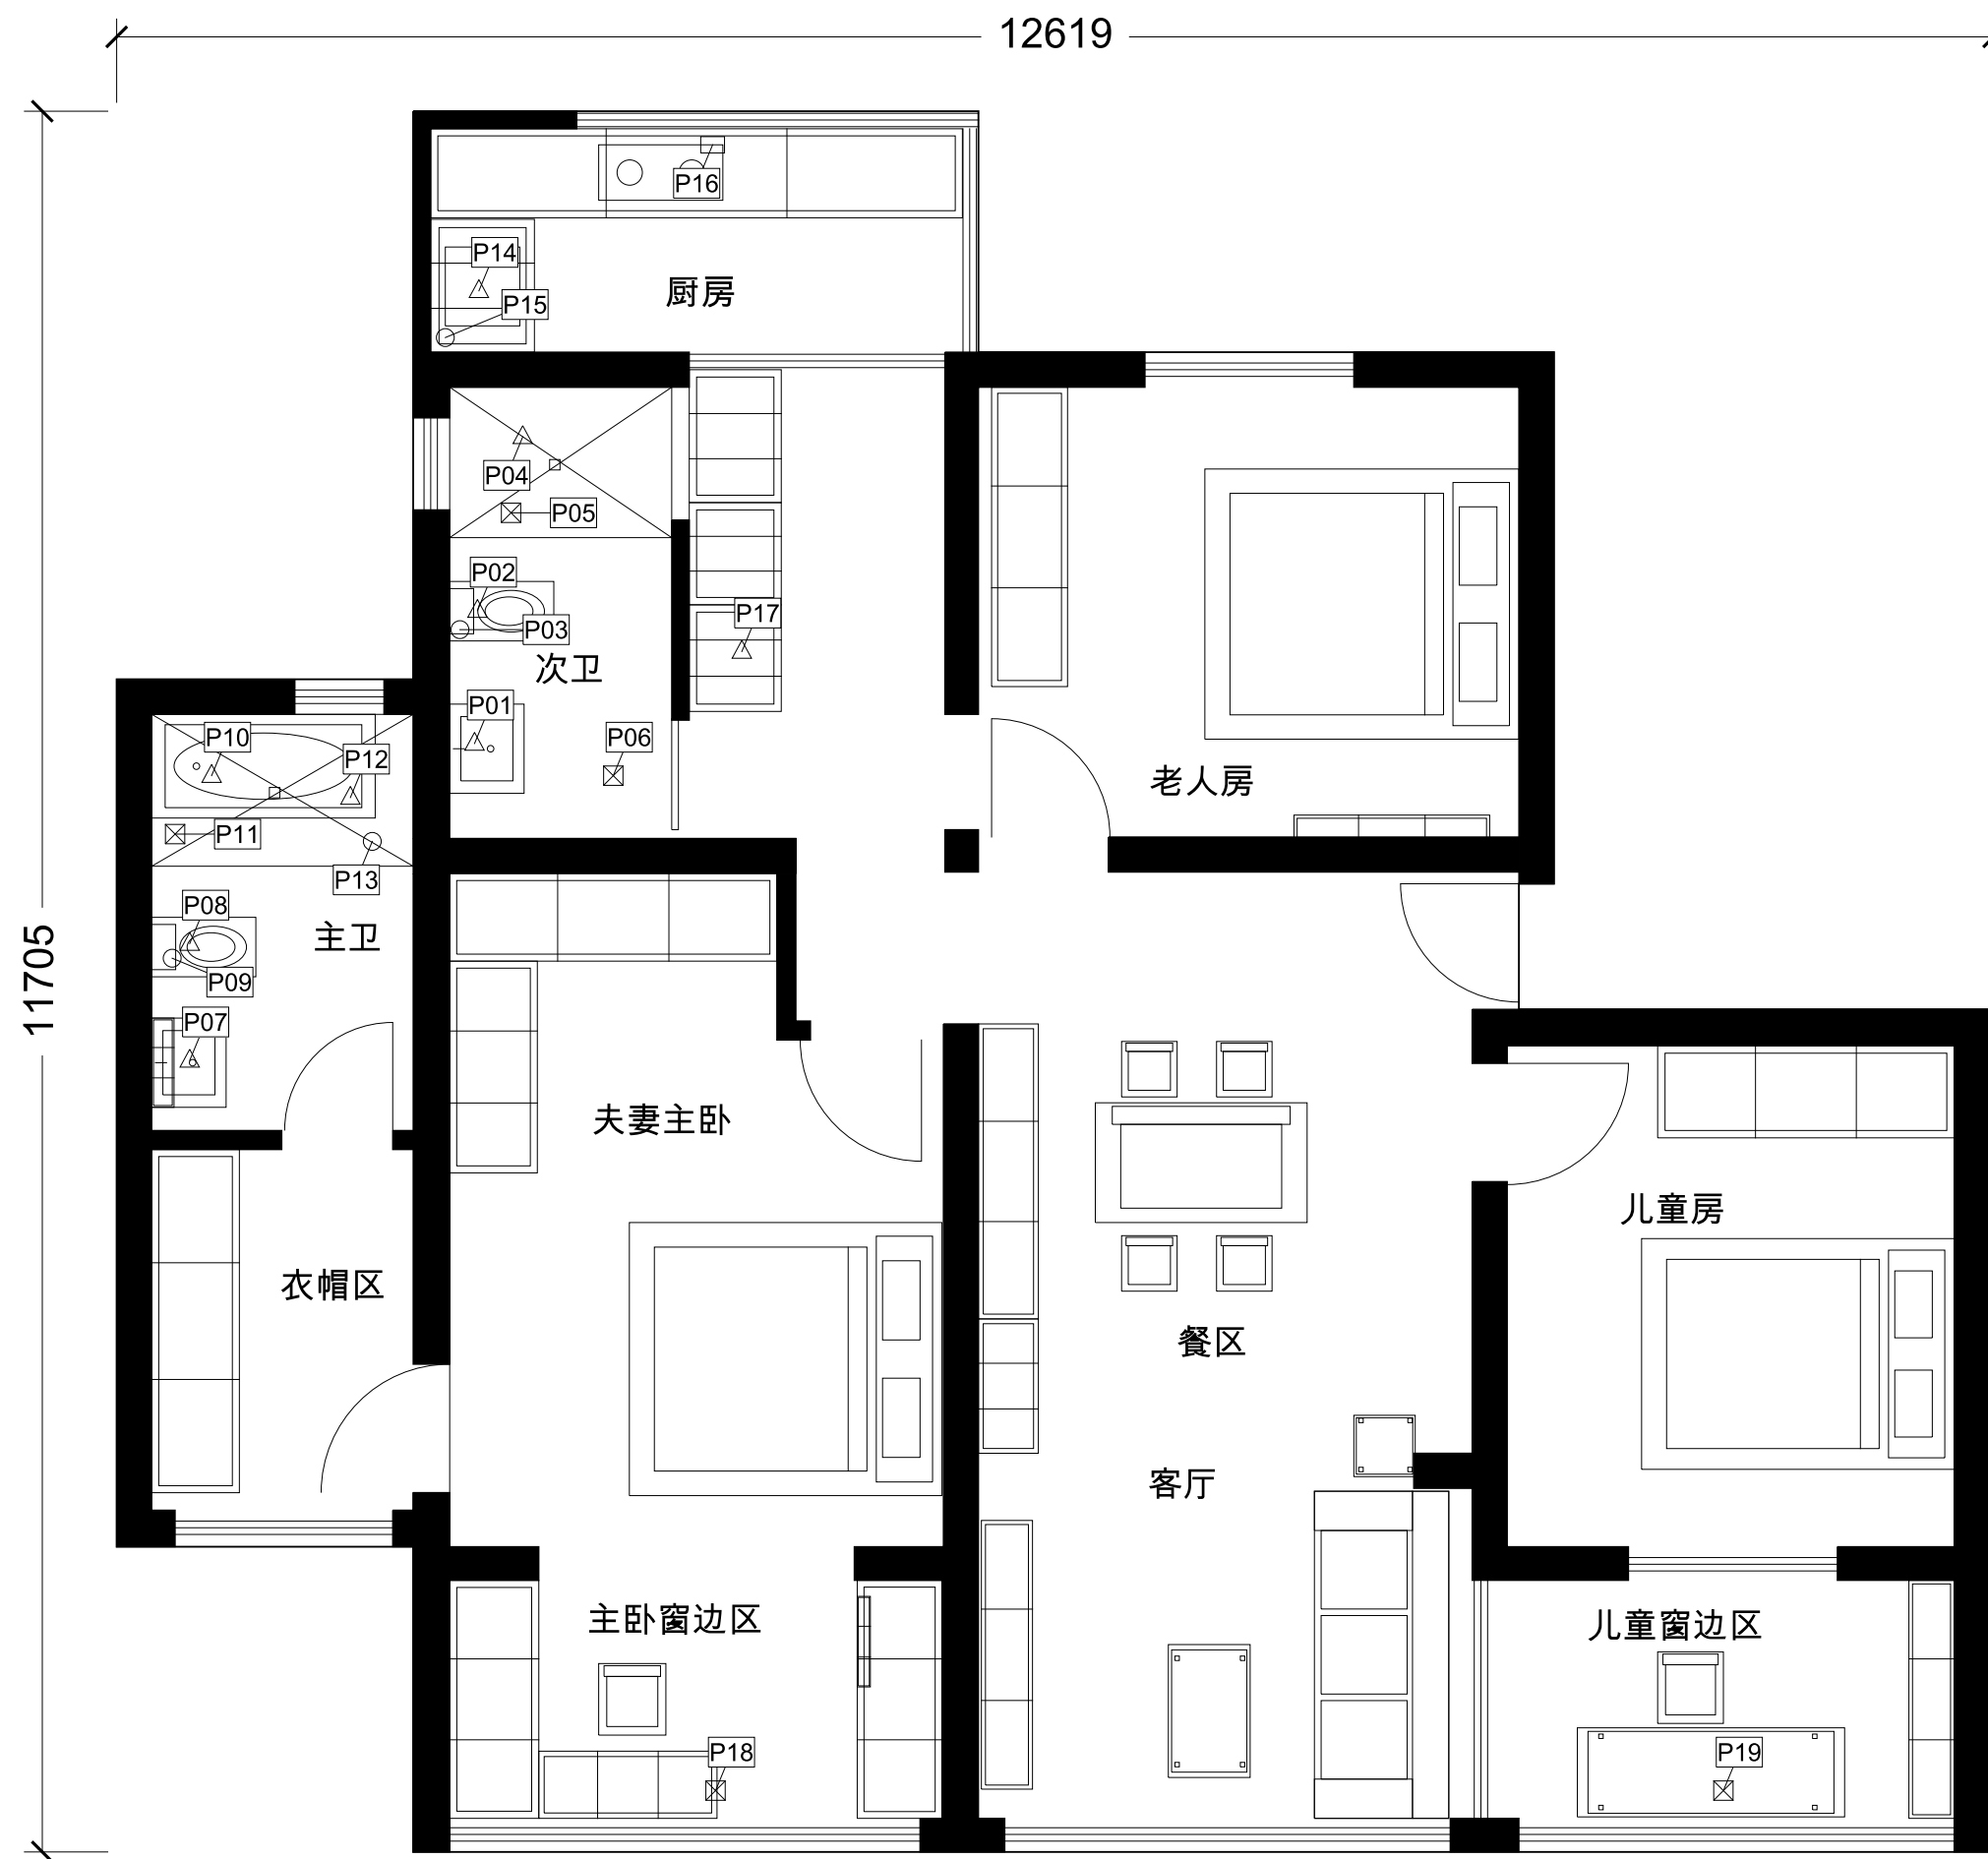

## 图纸说明 / NOTES

设计新增点位 / 全部待现场及产品复核  
详见同名CSV：编号、用途、X/Y定位坐标(mm)

P01 台盆 冷热H450 排水H300(墙排待确认)  
X 2406 / Y 7453

P02 马桶 给水H200  
X 2426 / Y 8347

P03 马桶排污 坑距300/400待确认  
X 2306 / Y 8219

P04 淋浴 冷热H1050  
X 2730 / Y 9516

P05 淋浴地漏 DN50  
X 2651 / Y 9005

P06 干区地漏 DN50  
X 3339 / Y 7237

P07 台盆 冷热H450 排水H300(墙排待确认)  
X 491 / Y 5322

P08 马桶 给水H200  
X 491 / Y 6108

P09 马桶排污 坑距300/400待确认  
X 373 / Y 6010

P10 淋浴 冷热H1050  
X 638 / Y 7237

P11 淋浴地漏 DN50  
X 393 / Y 6845

P12 浴缸 冷热H500+排水  
X 1571 / Y 7090

P13 浴缸地漏/排水  
X 1718 / Y 6795

P14 水槽 冷热H450 排水H300  
X 2435 / Y 10498

P15 净水/洗碗机排水预留  
X 2210 / Y 10183

P16 燃气热水器位 冷热+排烟 待确认  
X 4007 / Y 11480

P17 洗衣机 冷H1100+排水；干衣排水待确认  
X 4203 / Y 8072

P18 原阳台地漏 存废待确认  
X 4026 / Y 412

P19 原阳台地漏 存废待确认  
X 10802 / Y 412

定位原点：源图(200,1337)；X向东、Y向北。

未包含回路/管径/坡度计算，须机电深化。