

R1_BATH2_CLK — 次卫新隔墙 vs 旧衣帽间隔墙 | XY范围 (8500, 11900, 4200, 6900)


A · 现状基准 (原数字化图)

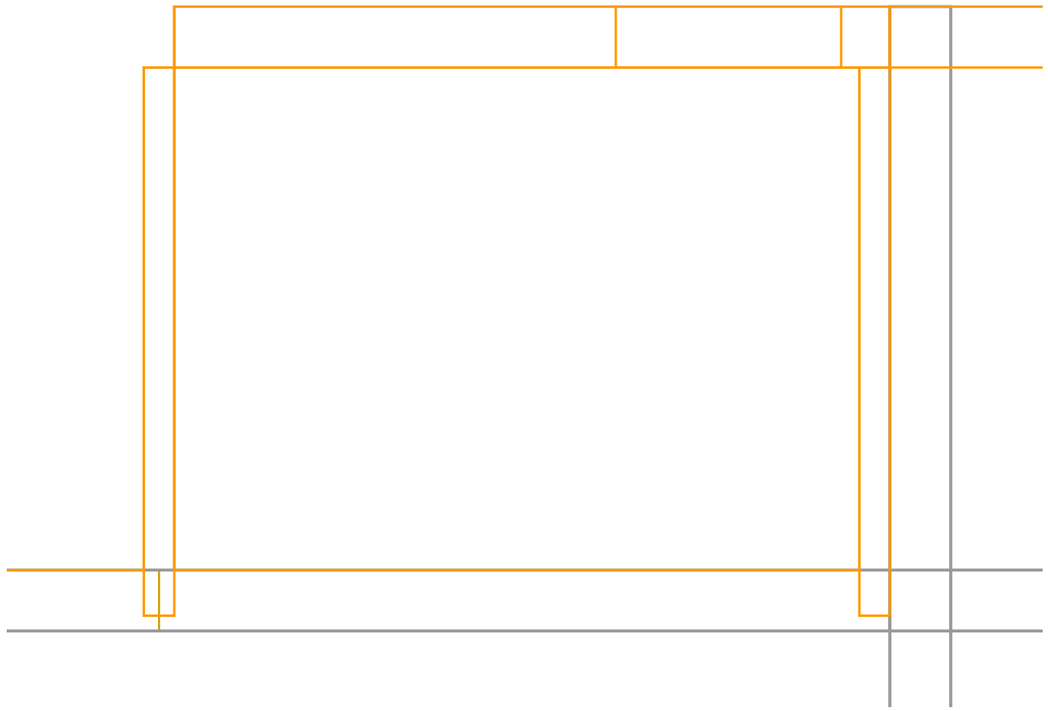


B · 拆改意图 (红虚=已批拆除 / 橙=待裁)

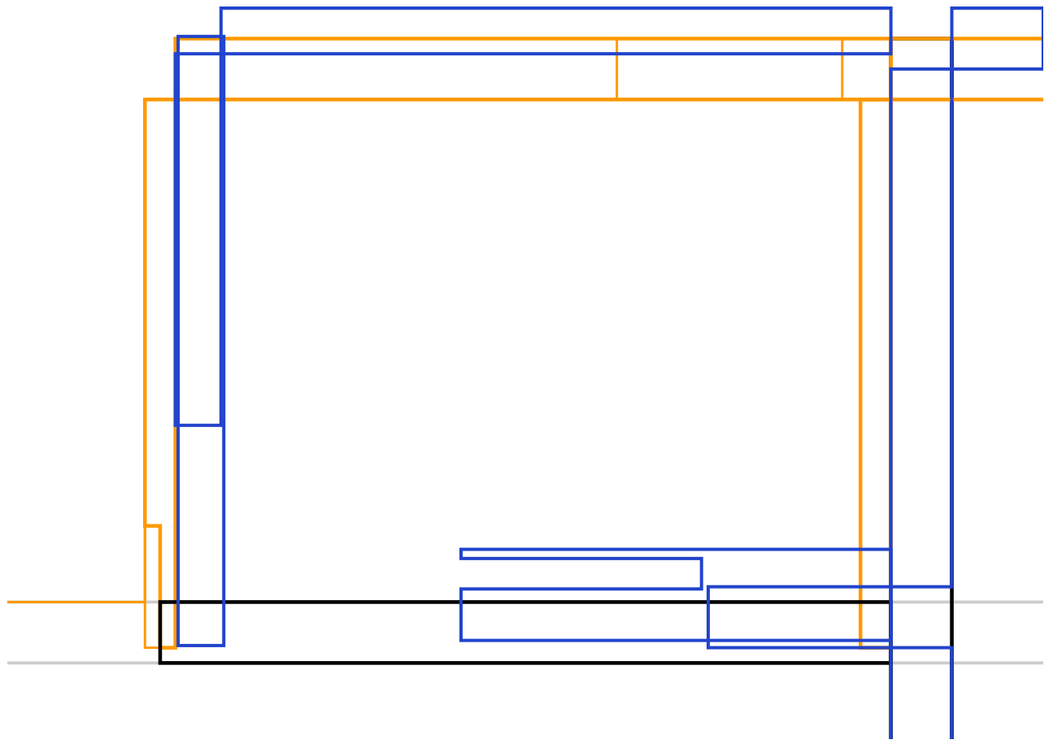

C · 已确认设计目标 (模型结构)

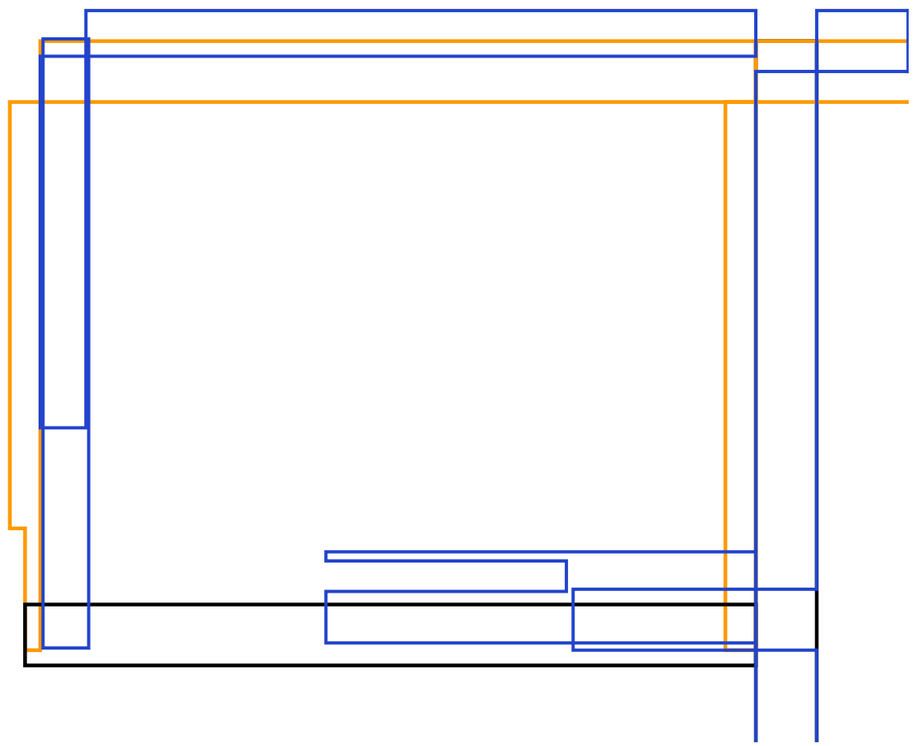


D · CAD 自动生成 V5 (品红=冲突候选)

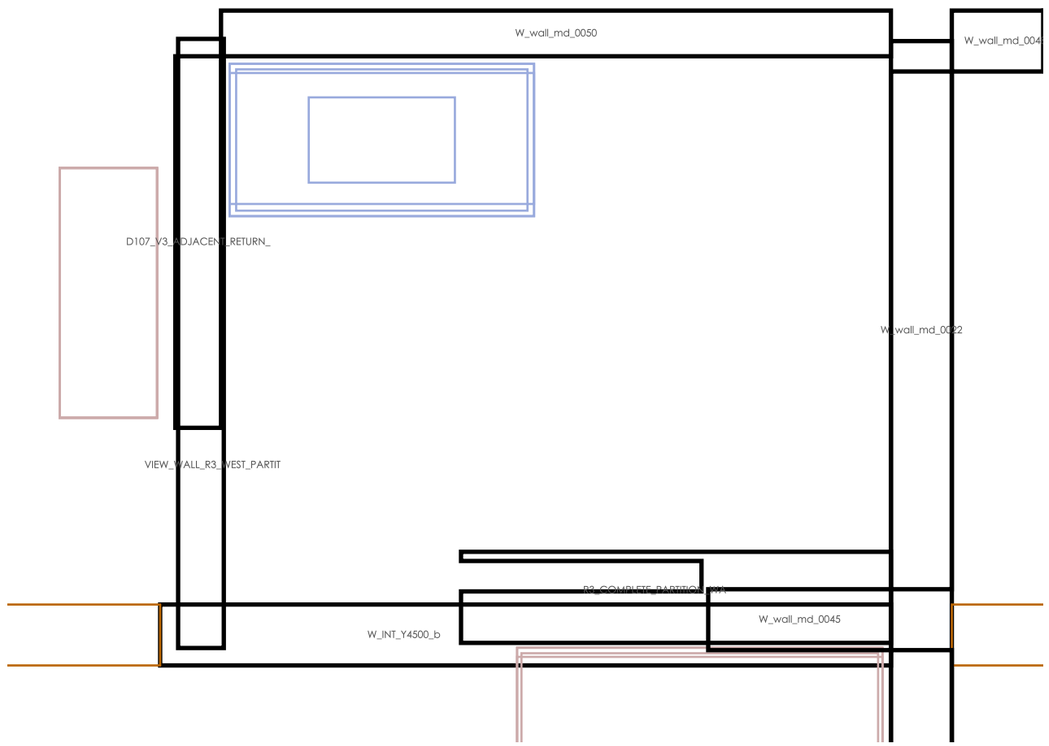


R1_BATH2_CLK 证据放大 (灰色原墙/黑保留/蓝新建/红拆/橙待裁/品红冲突)

① D107_V3_RED_SIDE_50MM_WALL [PROPOSED_NEW | 1650]
② DOOR_V2_D107_RIGHT_RETURN_WALL [PROPOSED_NEW | 1650]
③ R3_COMPLETE_PARTITION_WALLS [PROPOSED_NEW | 1650]
④ VIEW_WALL_R3_SOUTH_POCKET_PARTITIO [PROPOSED_NEW | 1650]
⑤ VIEW_WALL_R3_WEST_PARTITION [PROPOSED_NEW | 1650]
⑥ W_INT_CLK_E [DESIGN_REVIEW_PENDING | FC_SHELL]
⑦ W_INT_CLK_N [DESIGN_REVIEW_PENDING | FC_SHELL]
⑧ W_INT_CLK_W [DESIGN_REVIEW_PENDING | FC_SHELL]
⑨ W_INT_COR_N_STUB [UNVERIFIED | FC_SHELL]

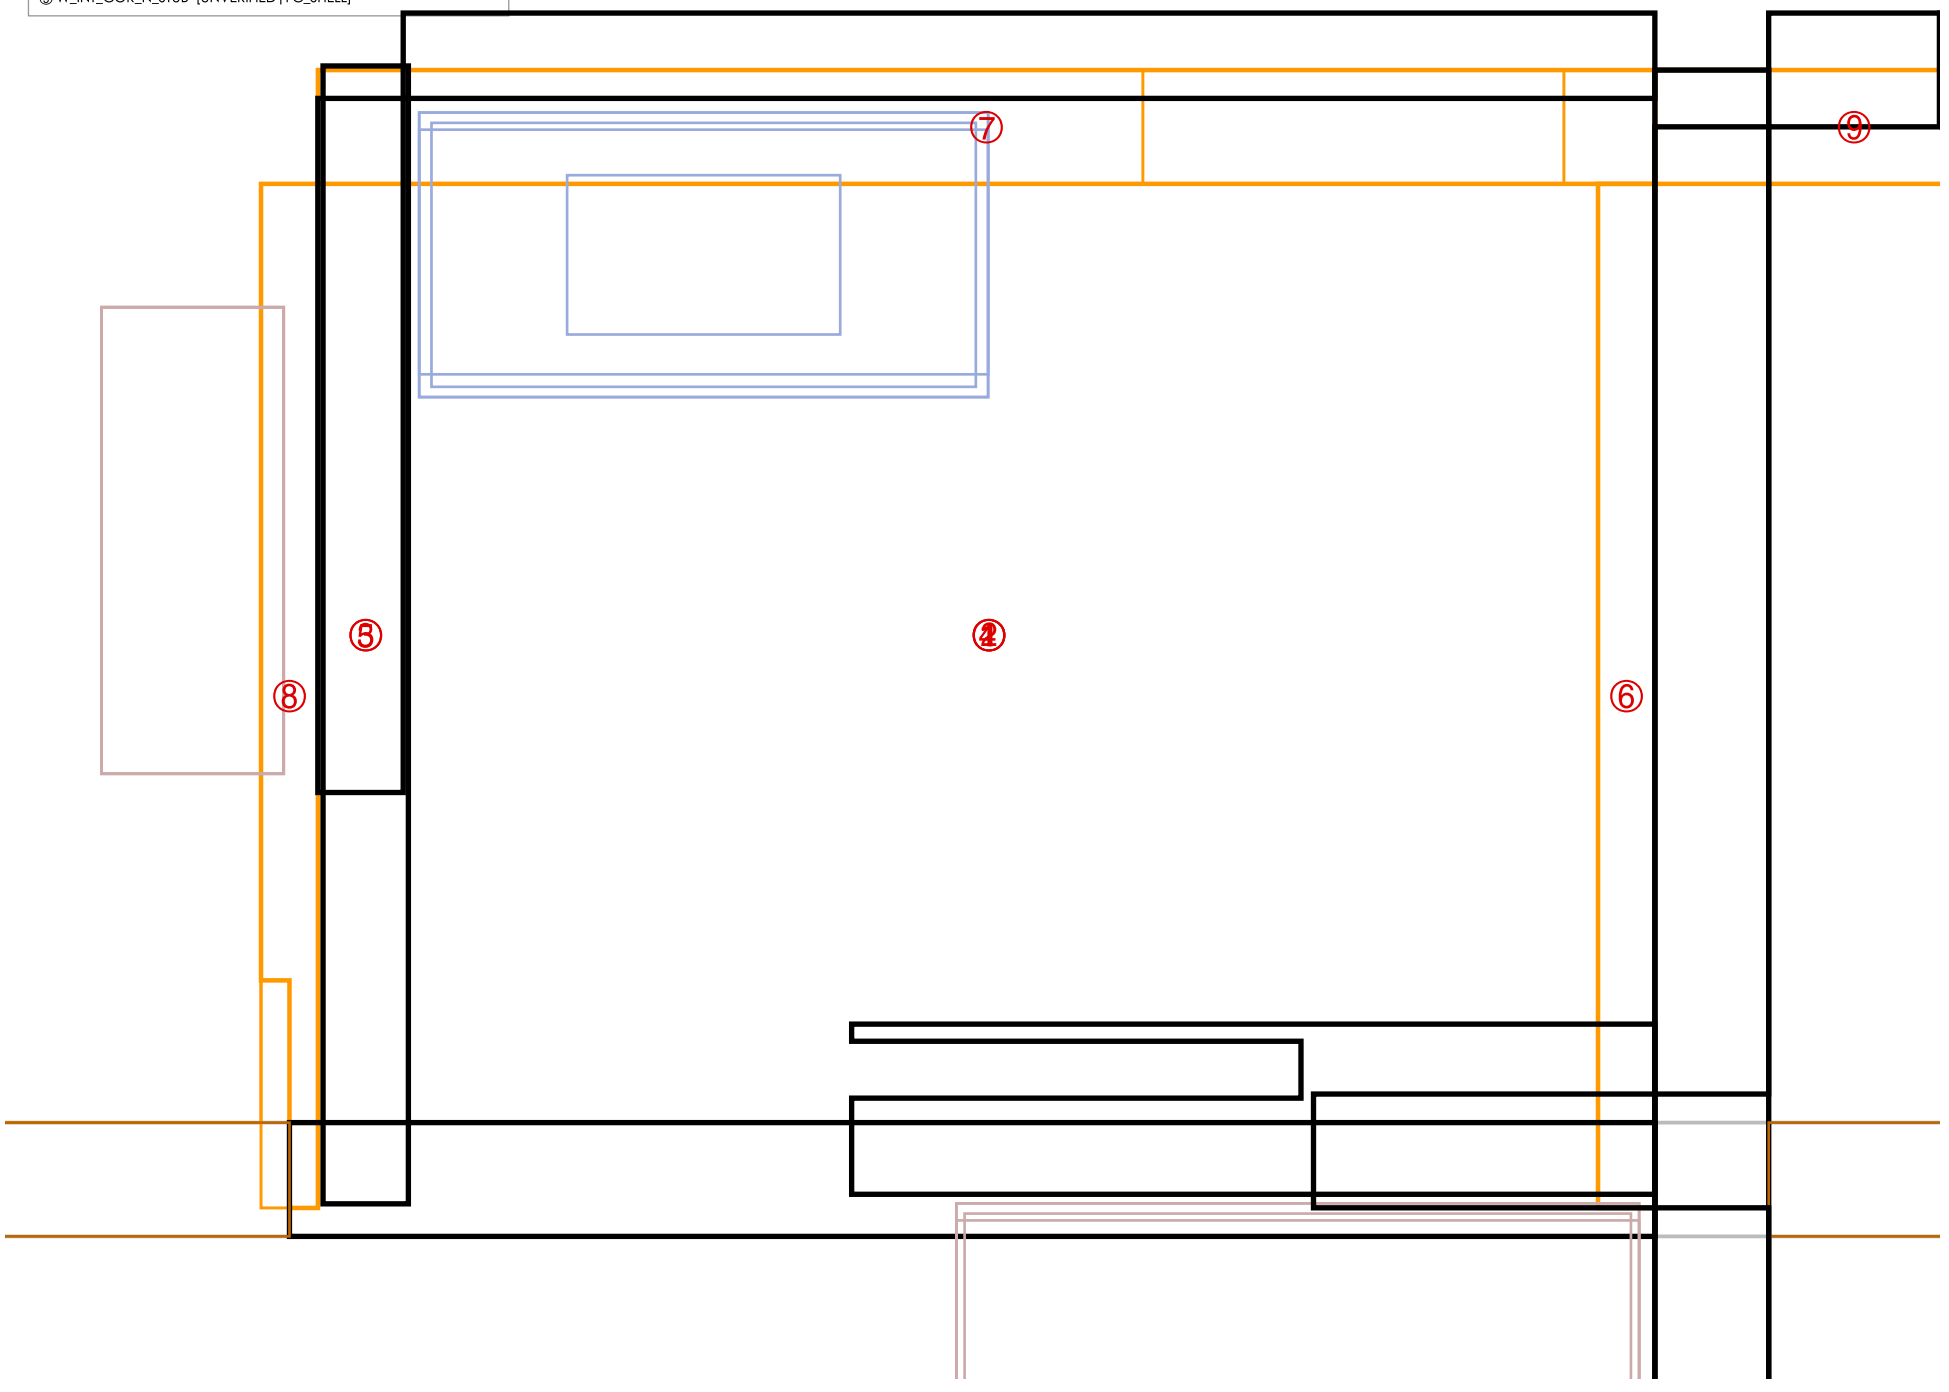


R2_KITCHEN — 厨房开放式拆改 + 残墙/门垛 | XY范围 (5400, 8300, 1400, 4800)


A · 现状基准 (原数字化图)

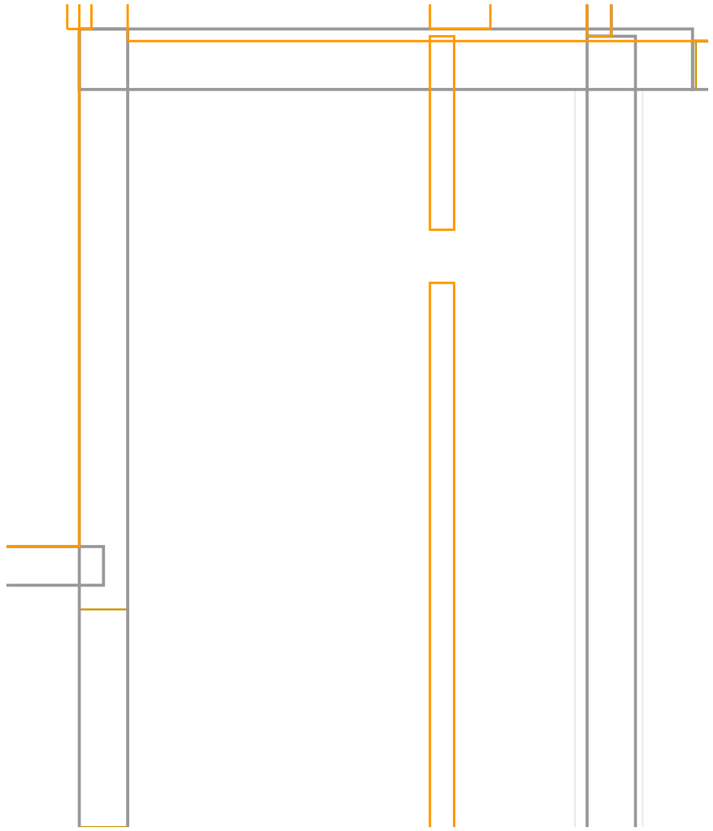


B · 拆改意图 (红虚=已批拆除 / 橙=待裁)

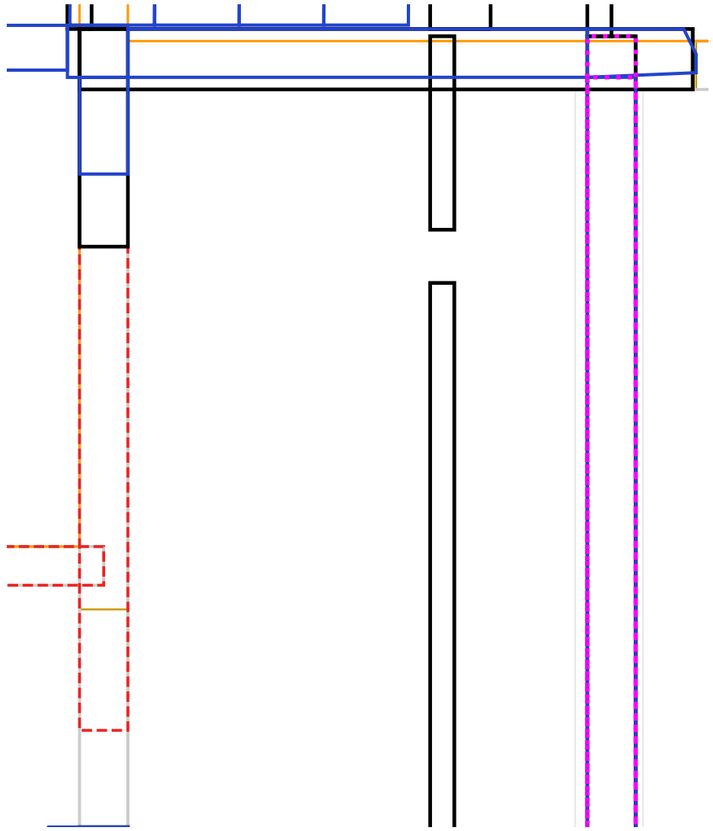


C · 已确认设计目标 (模型结构)

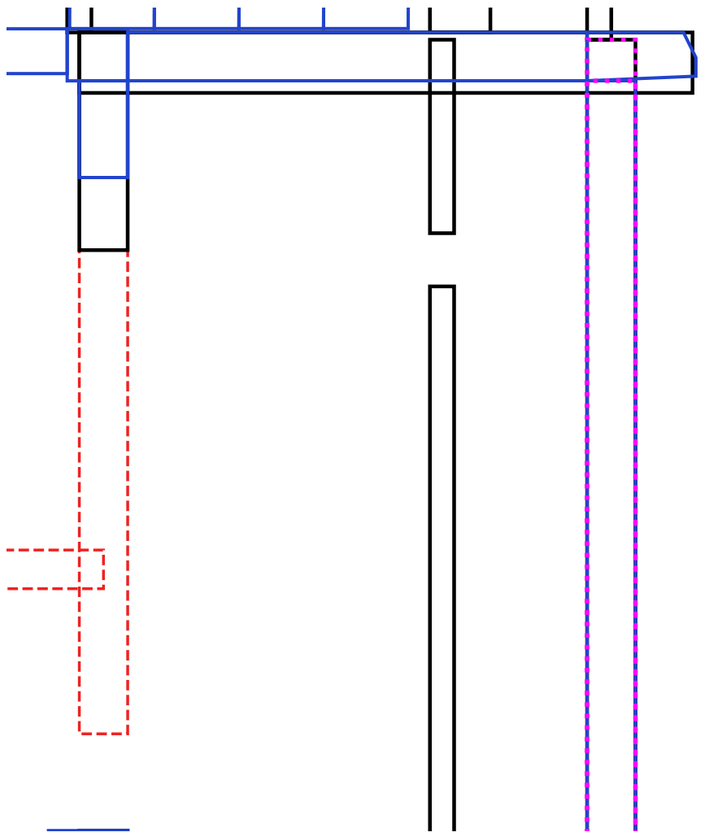

D · CAD 自动生成 V5 (品红=冲突候选)

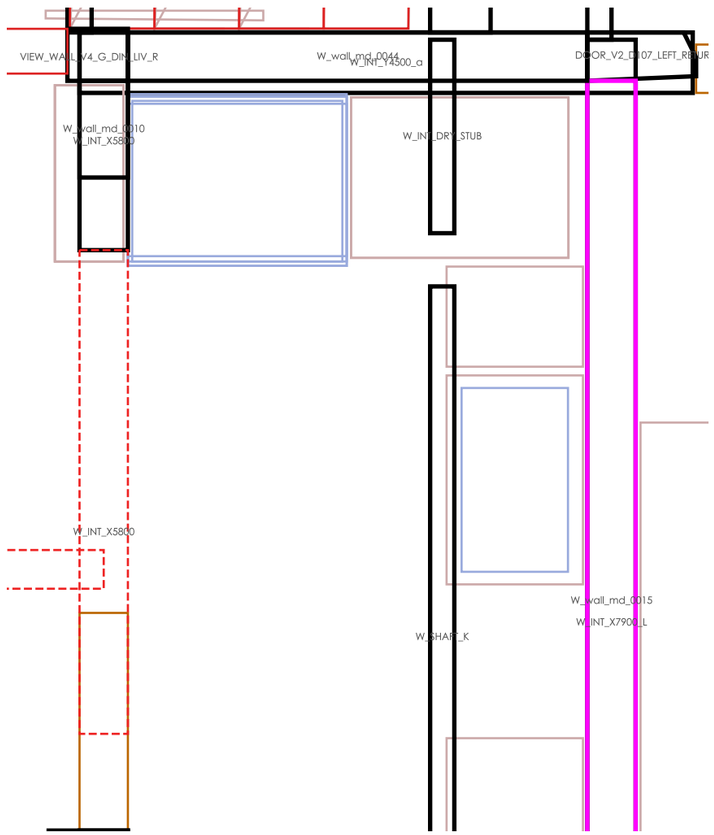


R2_KITCHEN 证据放大 (灰色原墙/黑保留/蓝新建/红拆/橙待裁/品红冲突)

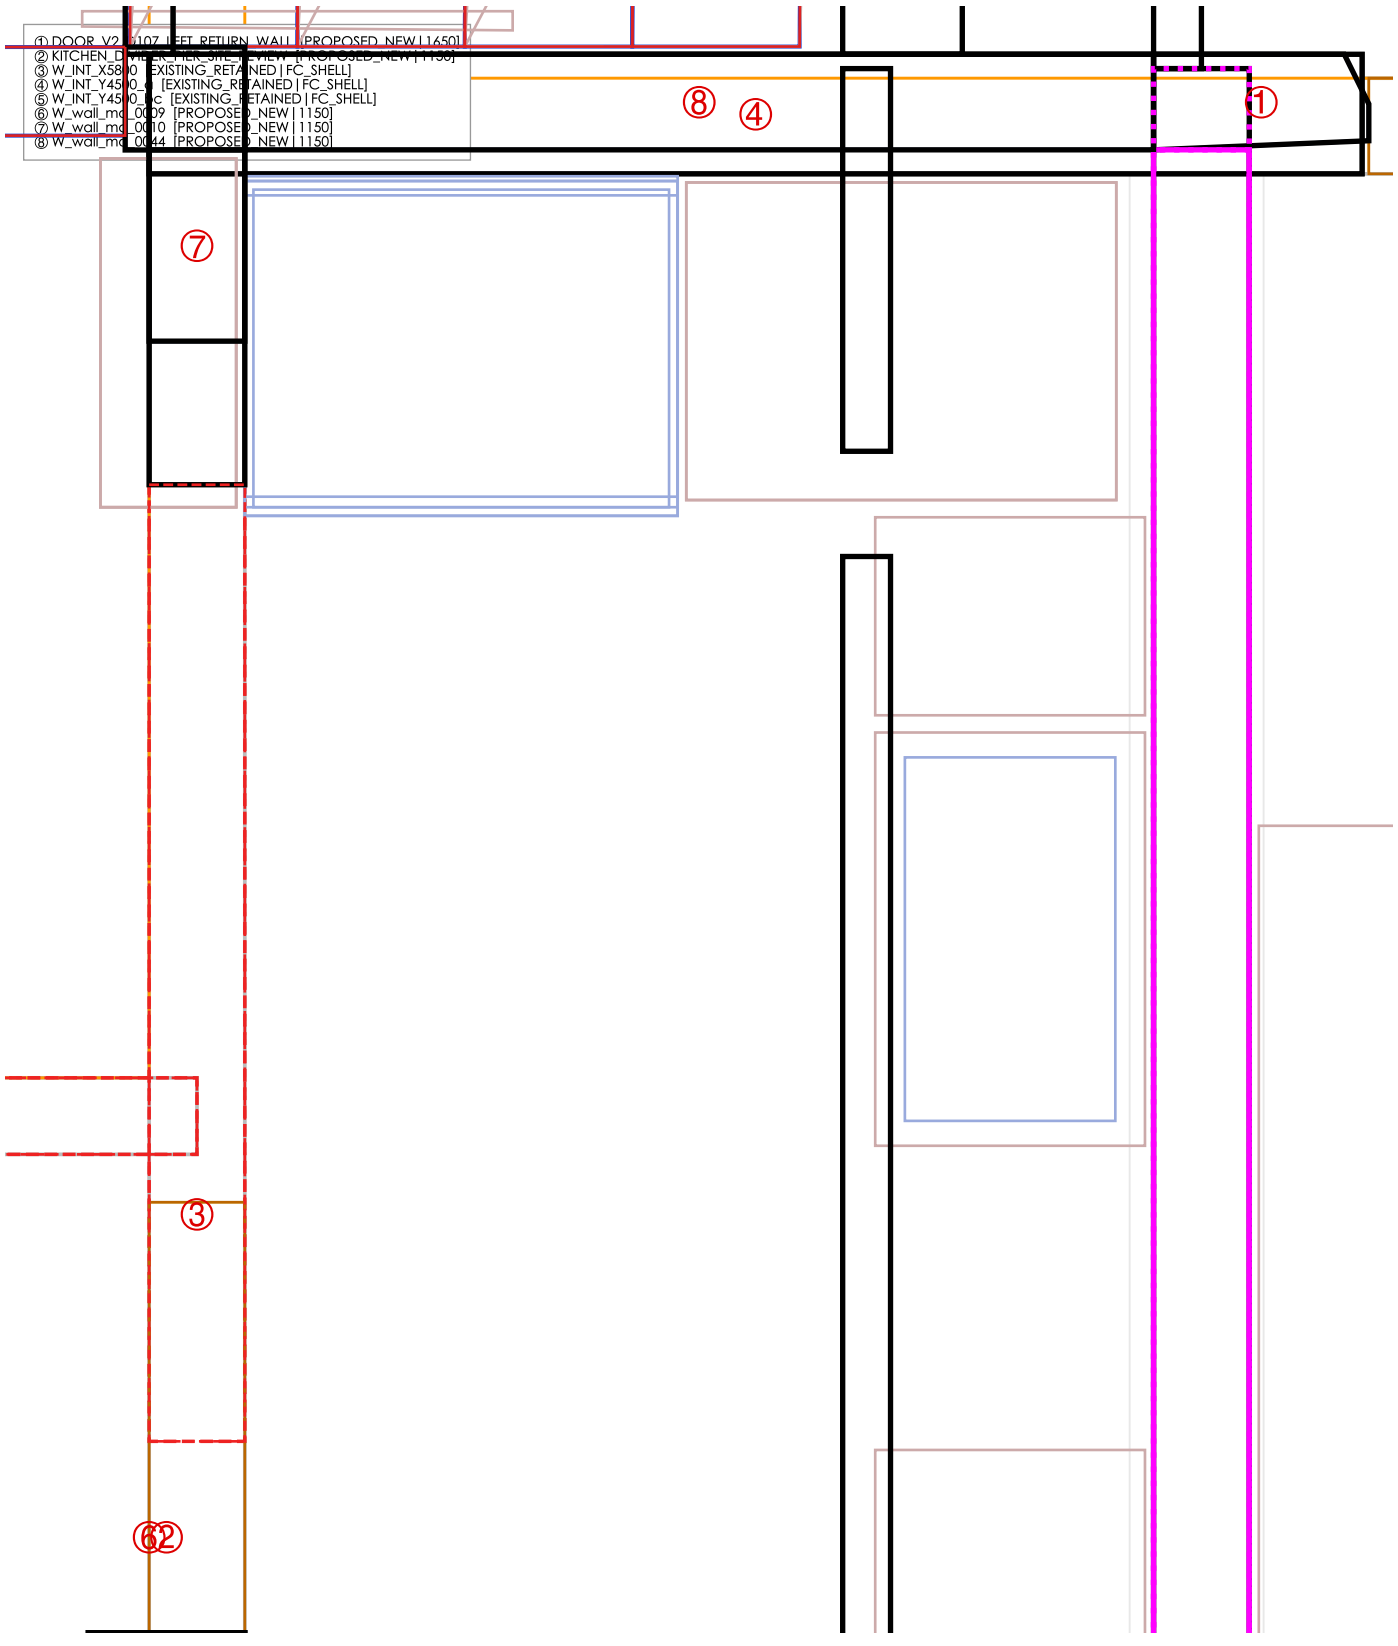


R3_STAIR — 走廊西墙开口(楼梯敞开) + 错层台阶 | XY范围 (7000, 9800, 4400, 8300)


A · 现状基准 (原数字化图)

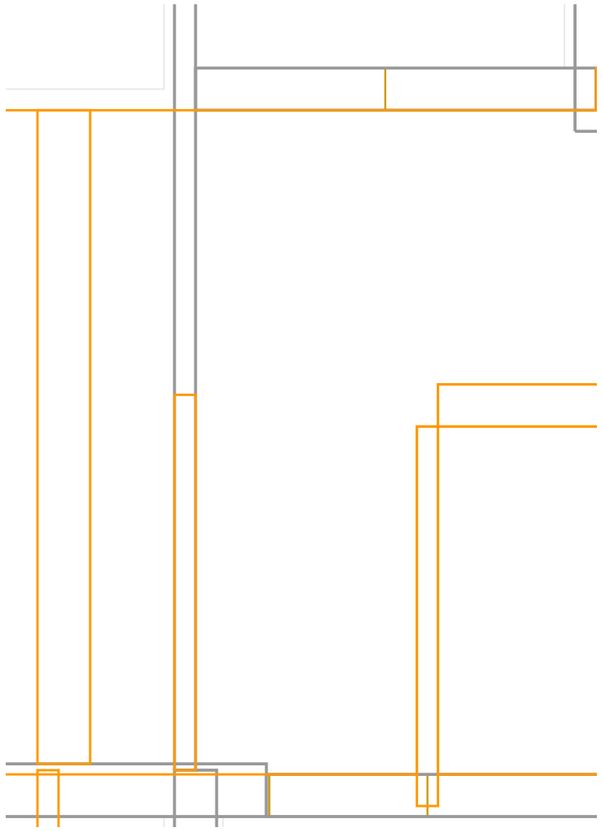


B · 拆改意图 (红虚=已批拆除 / 橙=待裁)

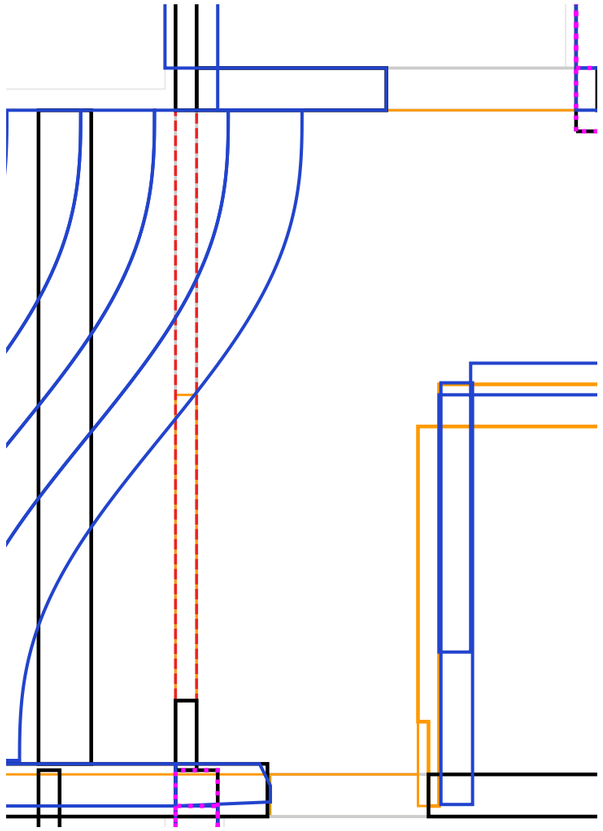


C · 已确认设计目标 (模型结构)

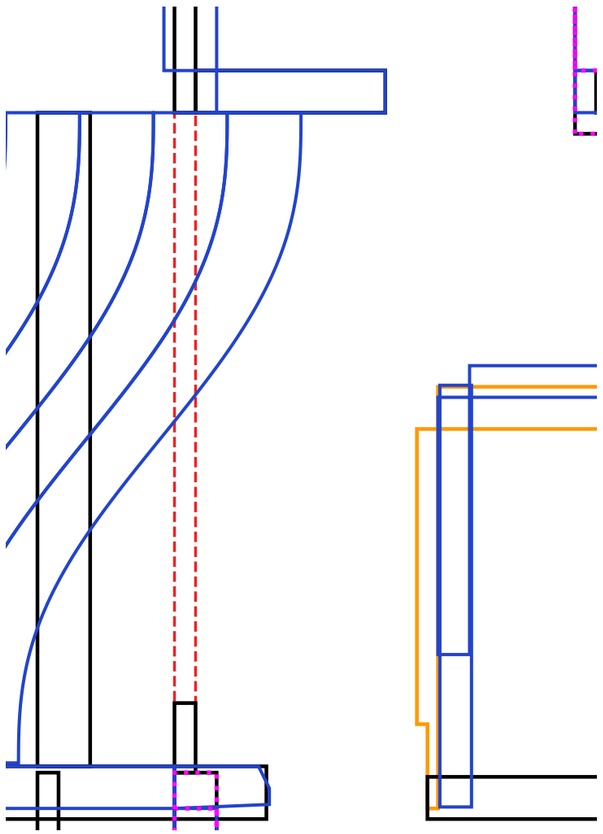

D · CAD 自动生成 V5 (品红=冲突候选)

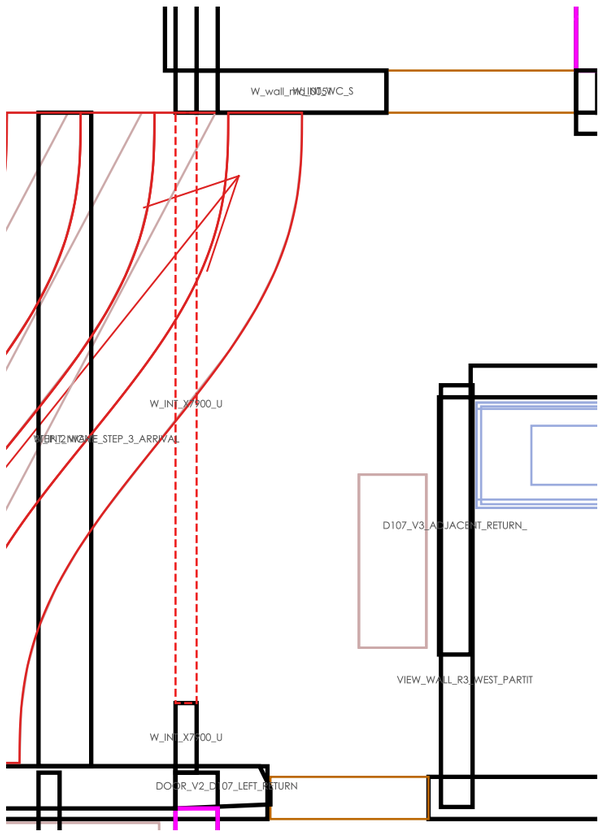

R3_STAIR 证据放大 (灰色原墙/黑保留/蓝新建/红拆/橙待裁/品红冲突)

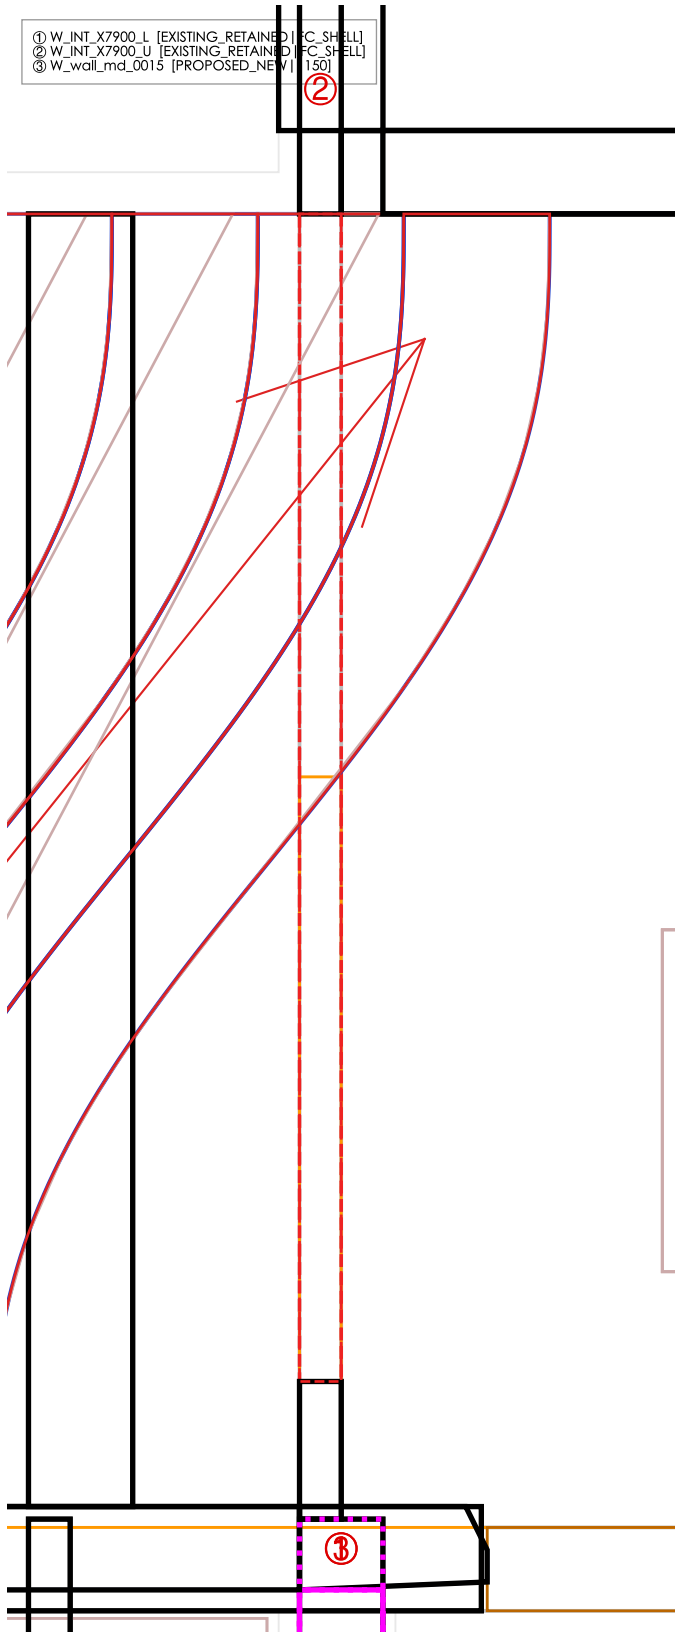


R4_NBALC — 北阳台拟建封窗 + 阳光房北带拆除 | XY范围 (7700, 13300, 12300, 14300)


A · 现状基准 (原数字化图)




B · 拆改意图 (红虚=已批拆除 / 橙=待裁)

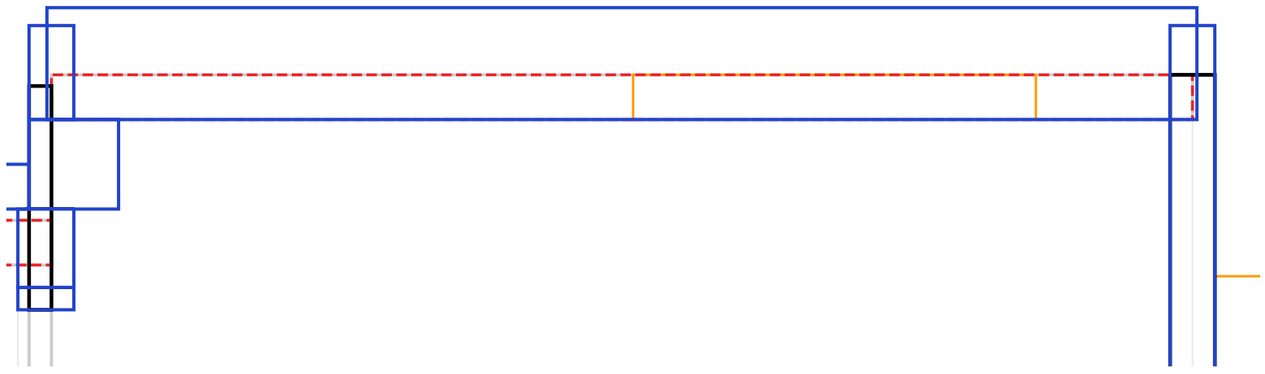


C · 已确认设计目标 (模型结构)

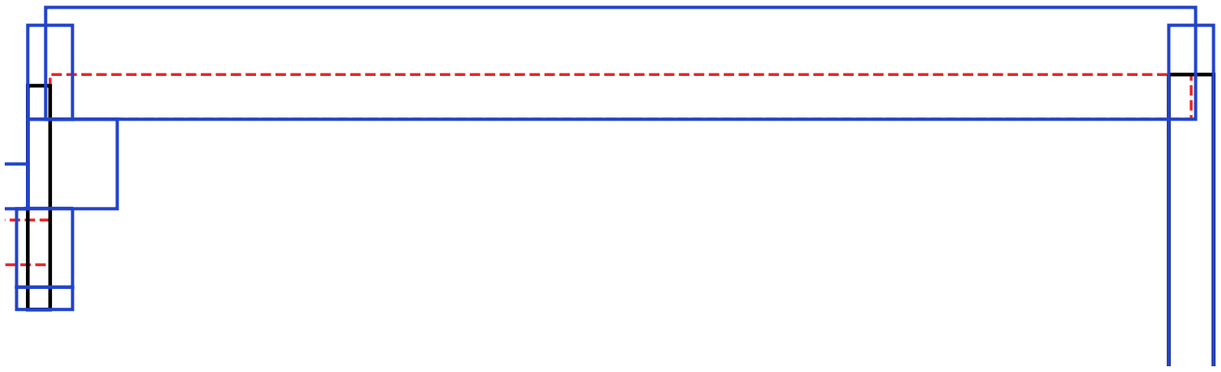

D · CAD 自动生成 V5 (品红=冲突候选)

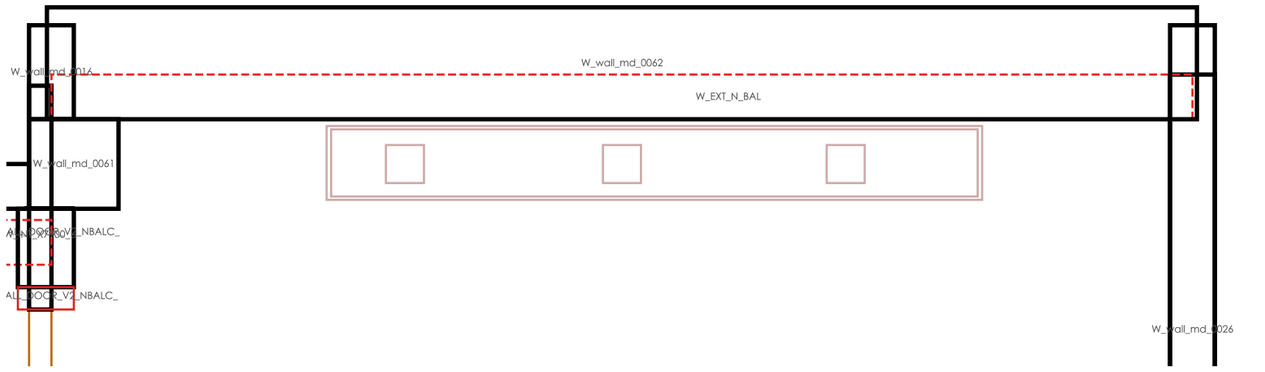


高度示意 (x-z)

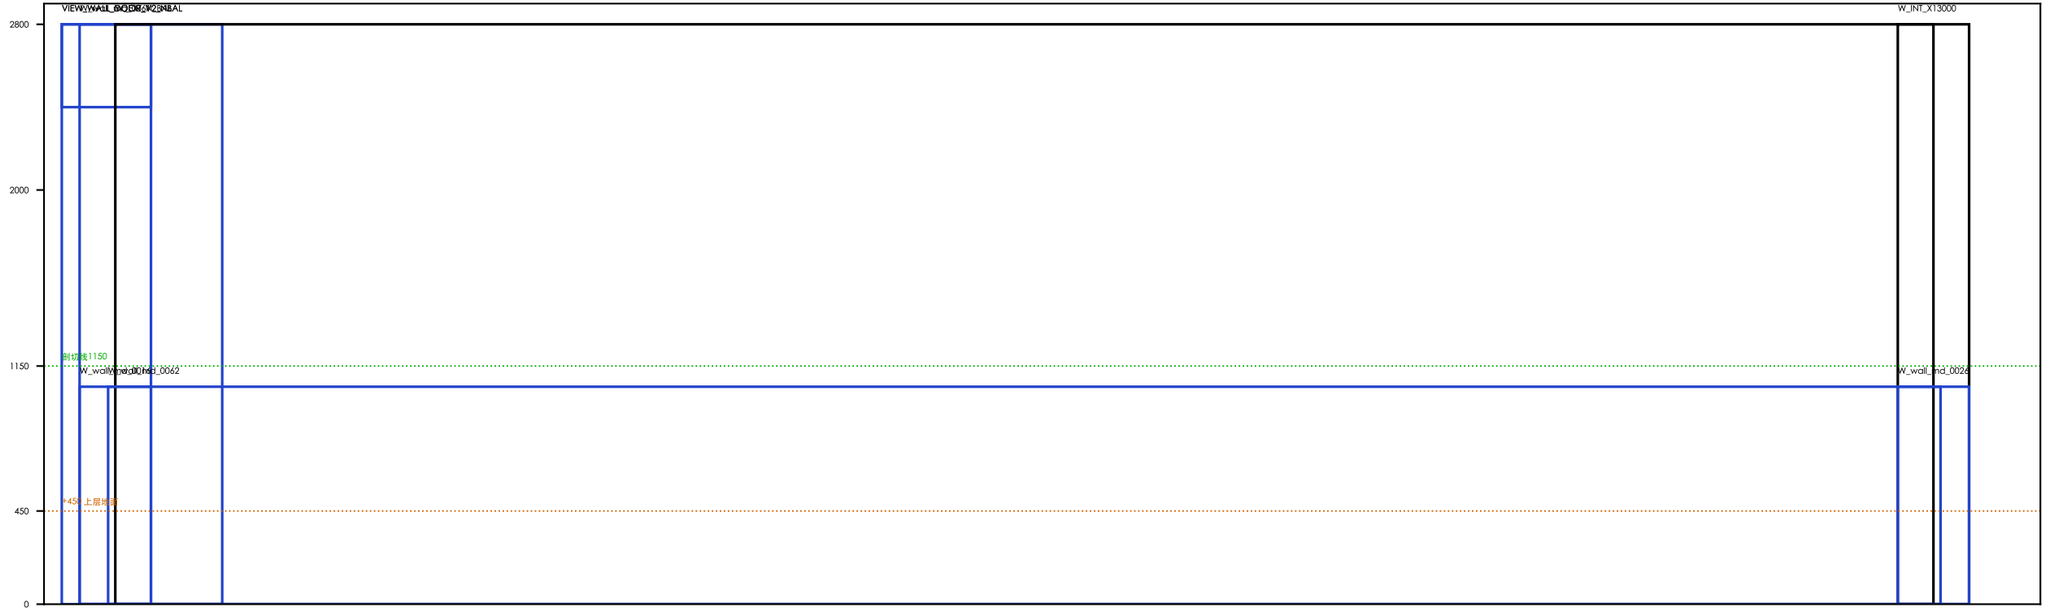
2800
2000
1150
450
0
W_INT_X13000
W_wall_Ind_0062
W_wall_Ind_0026
450 上层标高


R4_NBALC 证据放大 (灰色原墙/黑保留/蓝新建/红拆/橙待裁/品红冲突)

① VIEW_WALL_DOOR_V2_NBALC_NORTH_FULL [PROPOSED_NEW | FOOTPRINT_FALLBACK]
② VIEW_WALL_DOOR_V2_NBALC_SOLID_ABOV [PROPOSED_NEW | OVERHEAD_NOT_PLAN_WALL]
③ W_EXT_N_BAL [EXISTING_DEMOLISHED | FC]
④ W_INT_X13000 [EXISTING_RETAINED | FC_SHELL]
⑤ W_wall_md_0016 [PROPOSED_NEW | BELOW_CUT]
⑥ W_wall_md_0026 [PROPOSED_NEW | BELOW_CUT]
⑦ W_wall_md_0061 [PROPOSED_NEW | 1150]
⑧ W_wall_md_0062 [PROPOSED_NEW | BELOW_CUT]

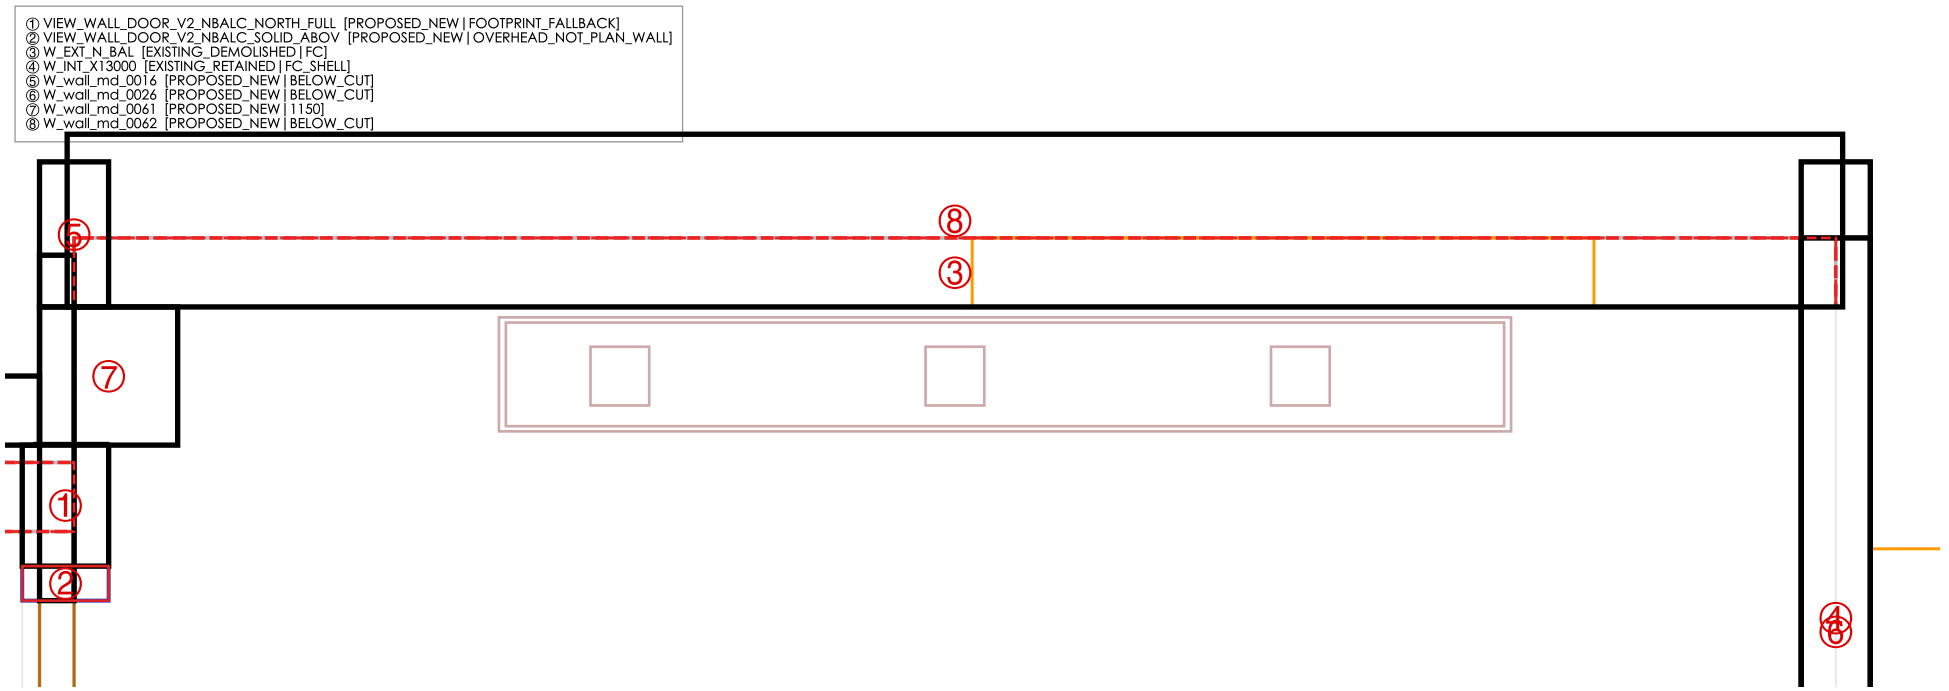


R5_BED_STUDY — 卧室/书房/客卧新隔墙 vs 原内墙 | XY范围 (9500, 13300, 4300, 11800)


A · 现状基准 (原数字化图)

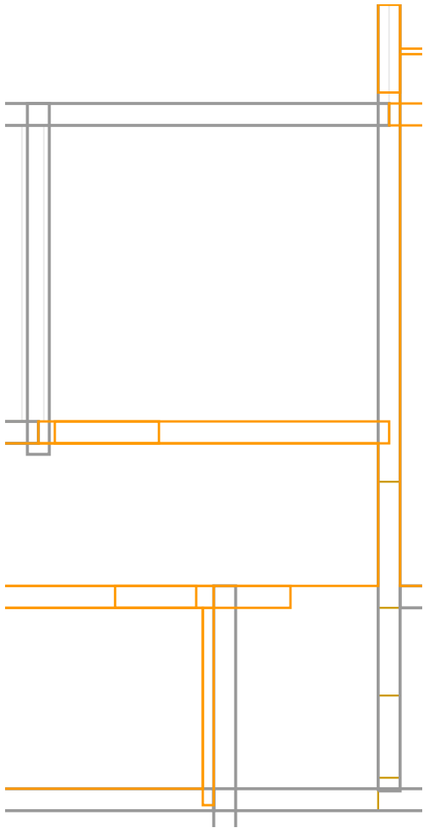


B · 拆改意图 (红虚=已批拆除 / 橙=待裁)

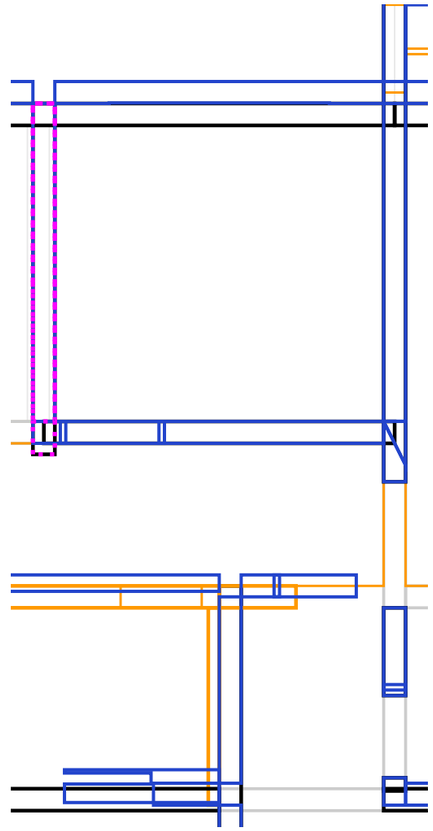


C · 已确认设计目标 (模型结构)

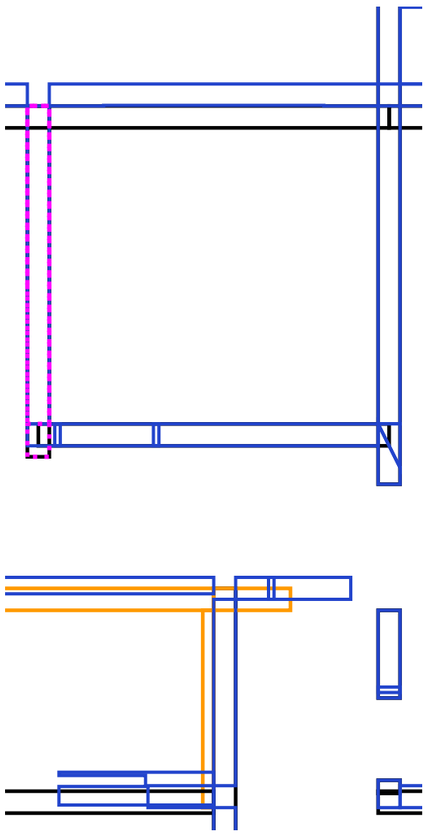

D · CAD 自动生成 V5 (品红=冲突候选)

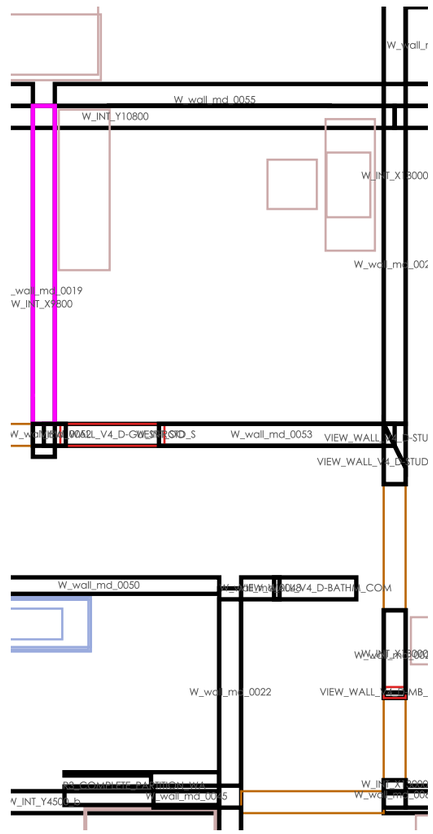


R5_BED_STUDY 证据放大 (灰色原墙/黑保留/蓝新建/红拆/橙待裁/品红冲突)

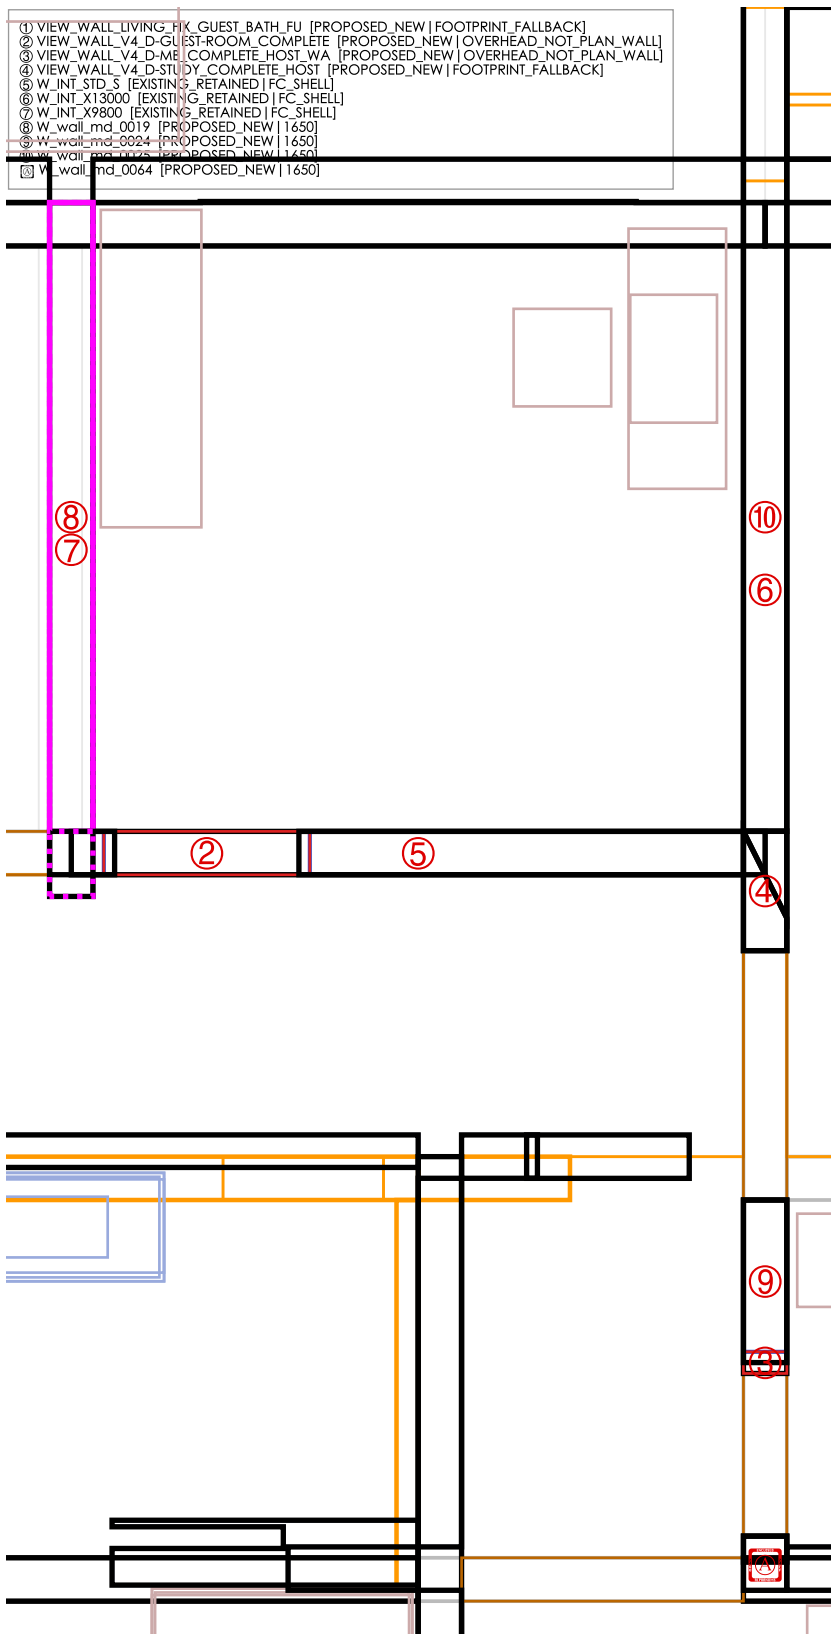


R6_ENT_WEST — 玄关/西侧外墙及入口墙段 | XY范围 (2300, 6000, 2200, 6600)


A · 现状基准 (原数字化图)

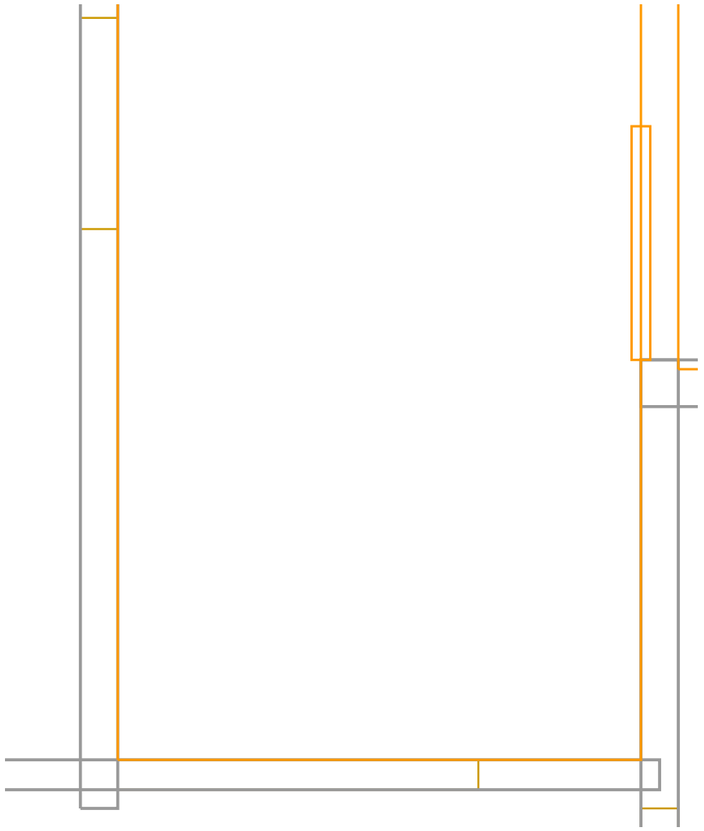


B · 拆改意图 (红虚=已批拆除 / 橙=待裁)

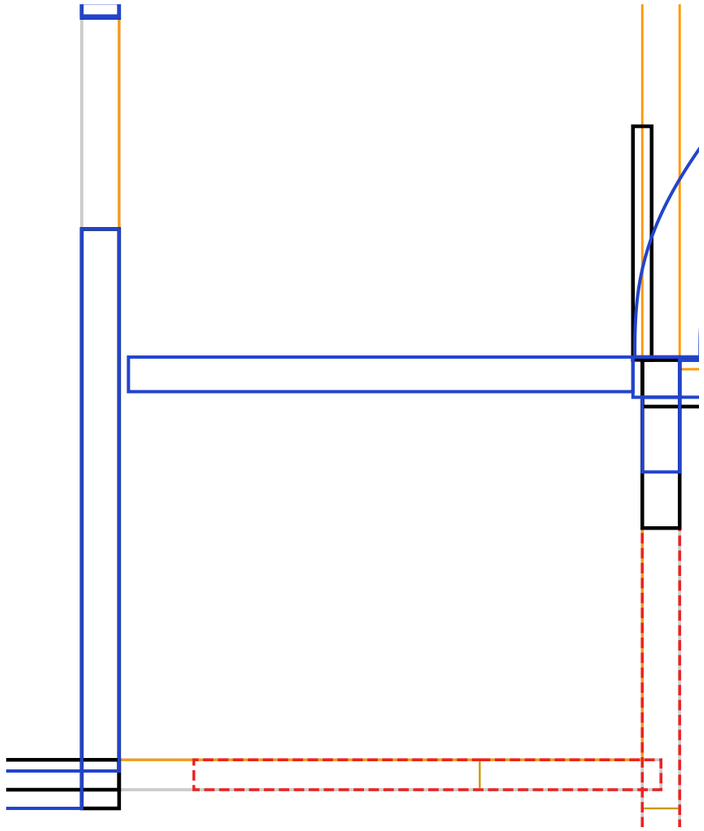

C · 已确认设计目标 (模型结构)

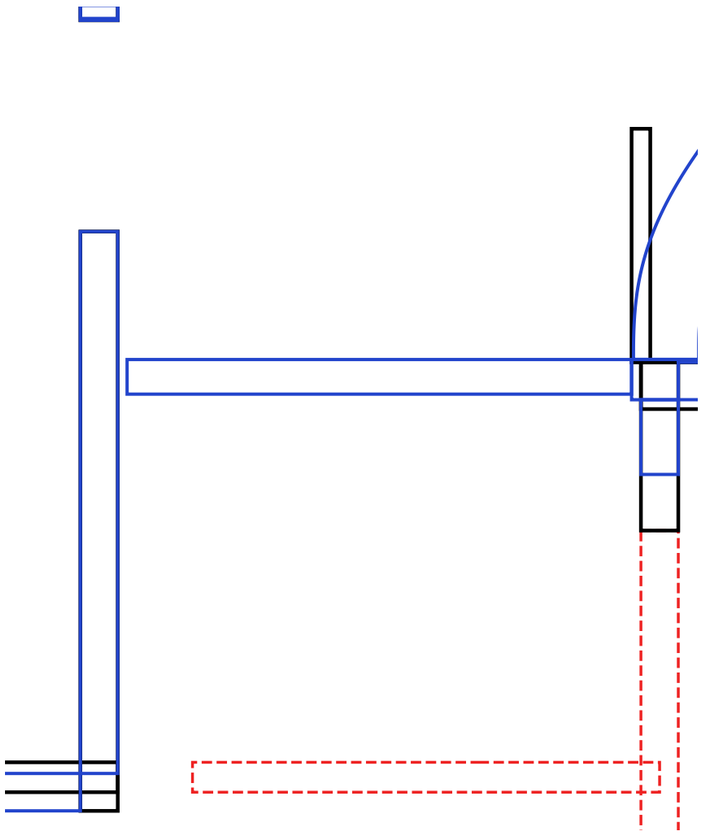


D · CAD 自动生成 V5 (品红=冲突候选)

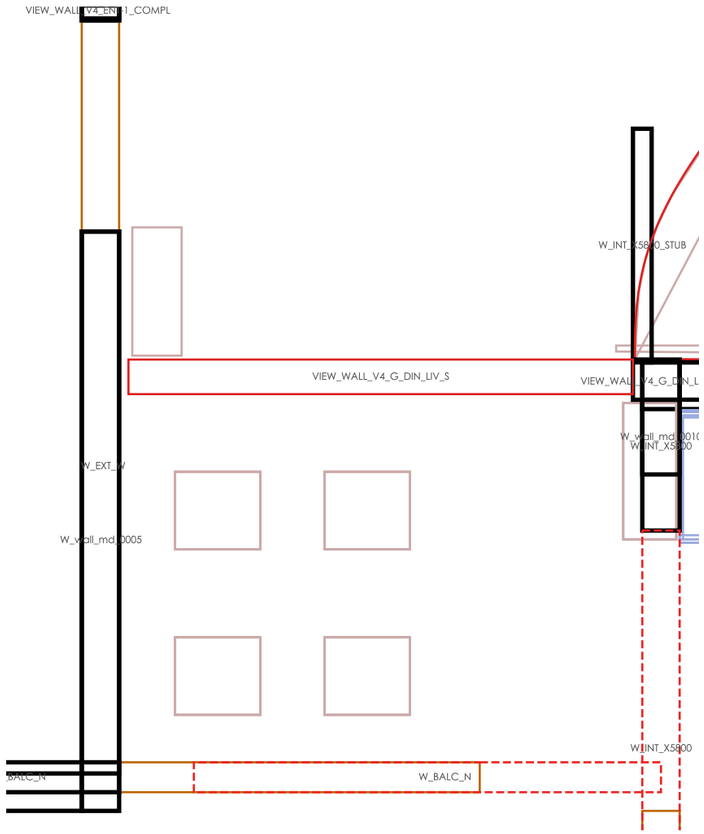


R6_ENT_WEST 证据放大 (灰色原墙/黑保留/蓝新建/红拆/橙待裁/品红冲突)

① VIEW_WALL_V4_ENT_COMPLETE_HOST_W [PROPOSED_NEW | FOOTPRINT_FALLBACK]
② VIEW_WALL_V4_G_DIN_LIV_RIGHT_PIER [PROPOSED_NEW | FOOTPRINT_FALLBACK]
③ W_BALC_W [EXISTING_RETAINED | FC_SHELL]
④ W_EXT_W [EXISTING_RETAINED | FC_SHELL]
⑤ W_wall_md_0004 [PROPOSED_NEW | BELOW_CUT]
⑥ W_wall_md_0005 [PROPOSED_NEW | 1150]
⑦ W_wall_md_0006 [PROPOSED_NEW | 1150]

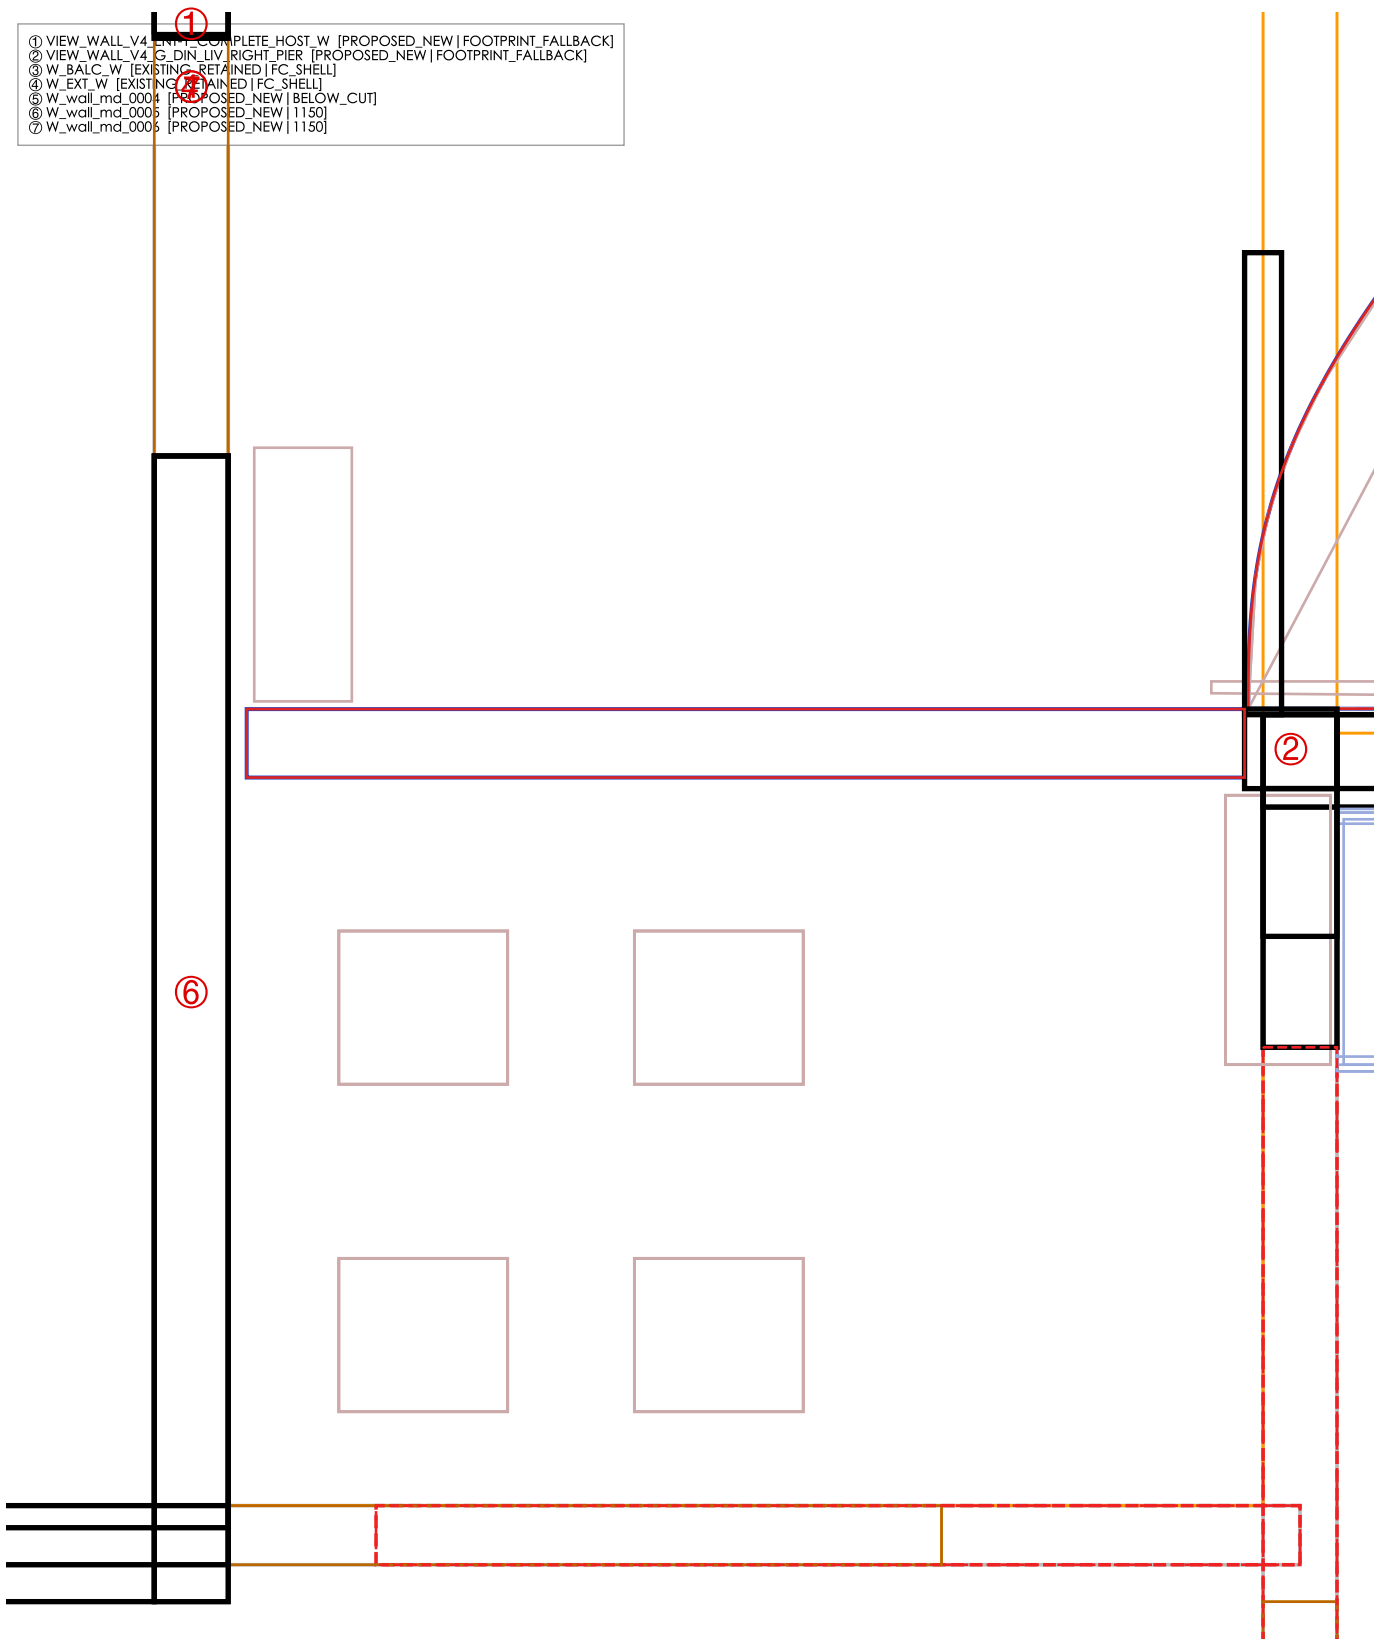


R7_BAY — 客厅飘窗头部/下部墙组合 | XY范围 (3400, 7300, 12500, 14000)


A · 现状基准 (原数字化图)

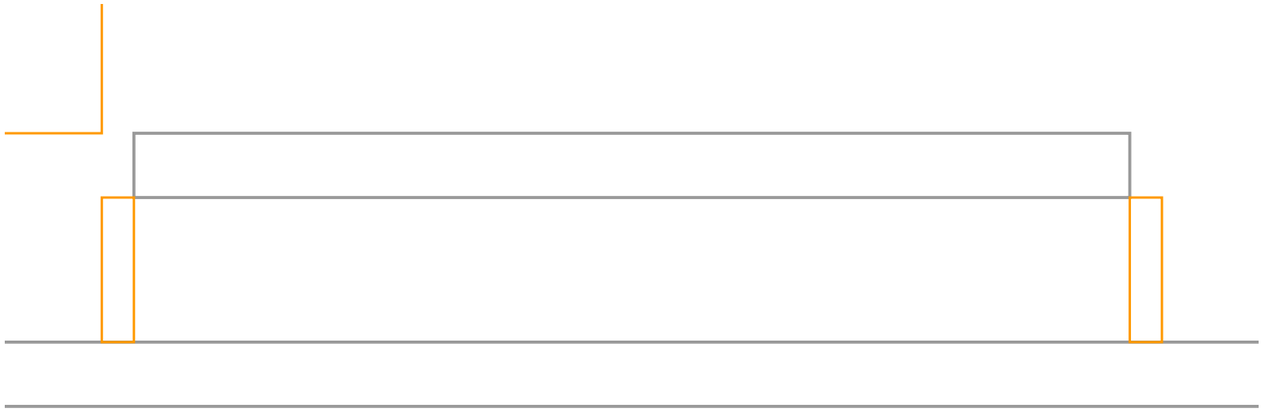


B · 拆改意图 (红虚=已批拆除 / 橙=待裁)

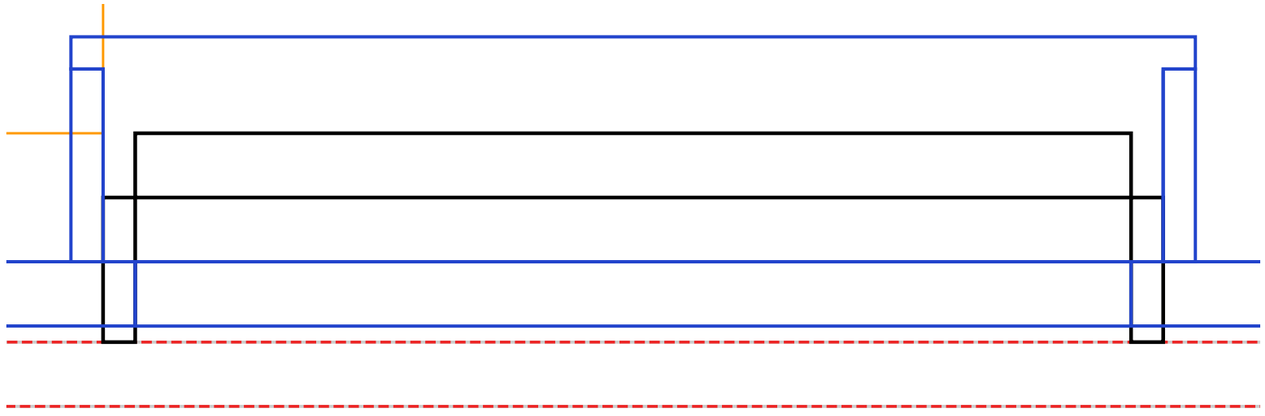


C · 已确认设计目标 (模型结构)

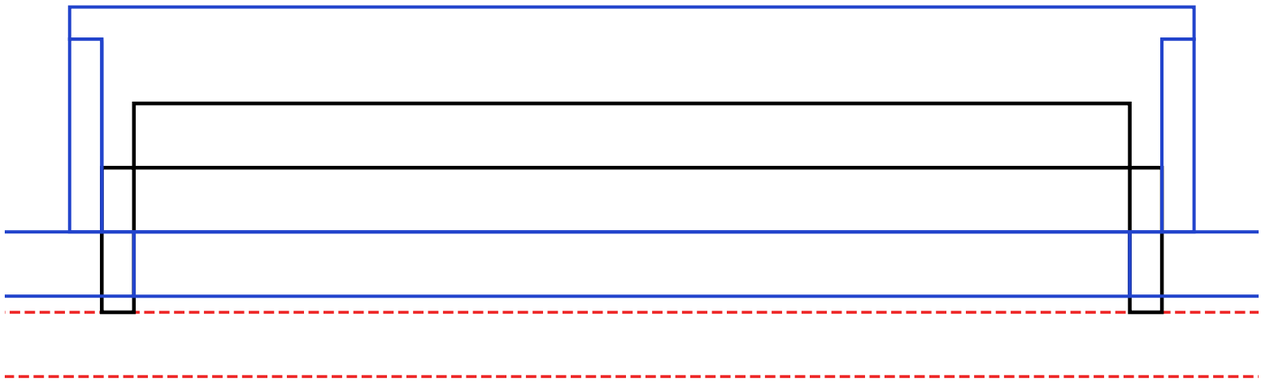


D · CAD 自动生成 V5 (品红=冲突候选)

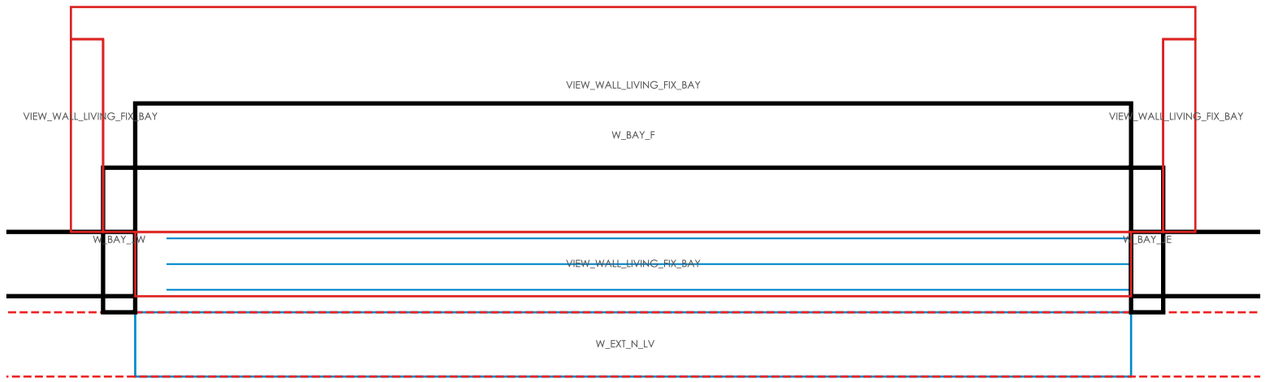

R7_BAY 证据放大 (灰色原墙/黑保留/蓝新建/红拆/橙待裁/品红冲突)

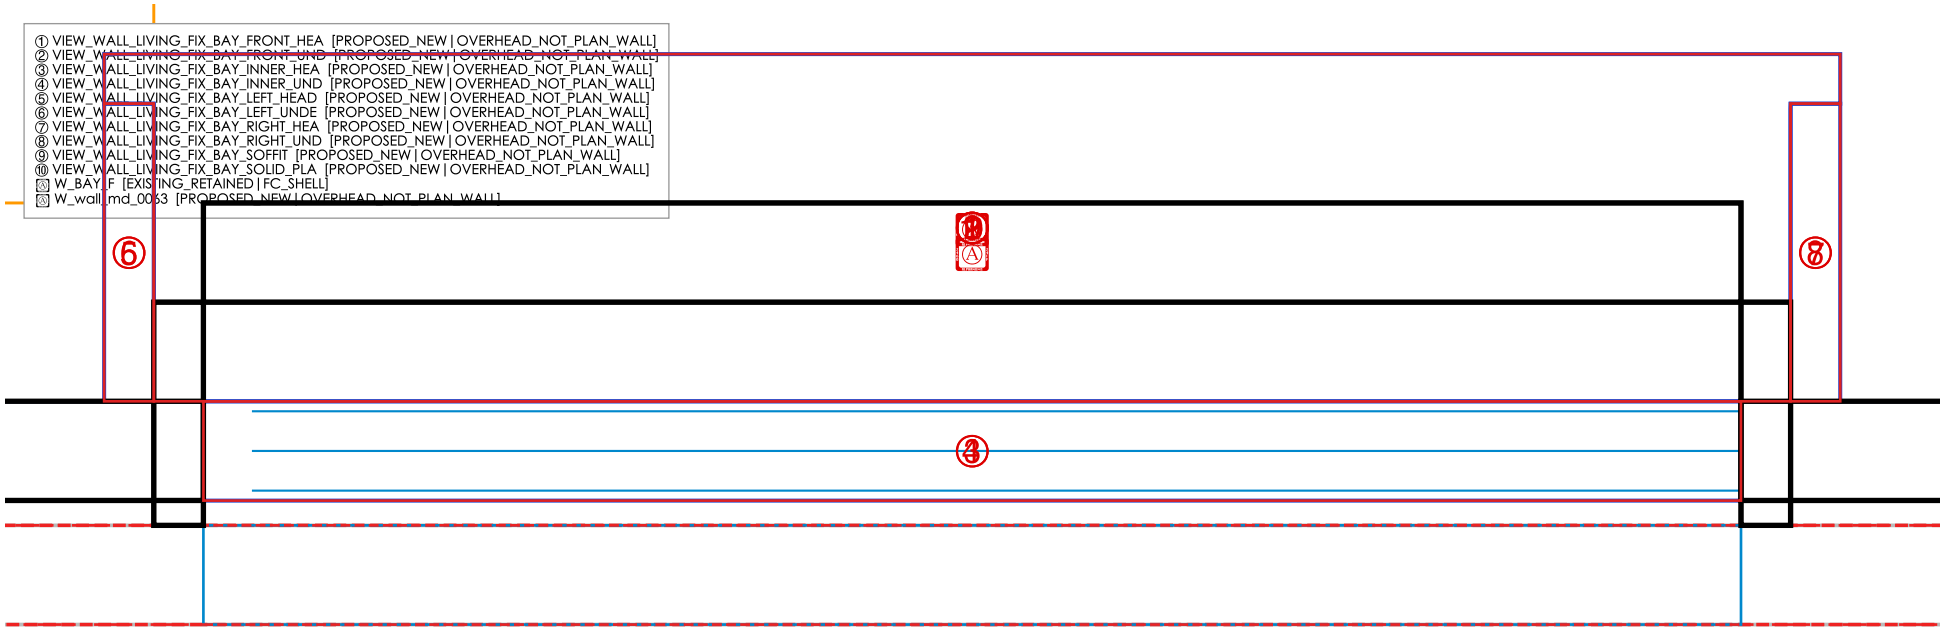

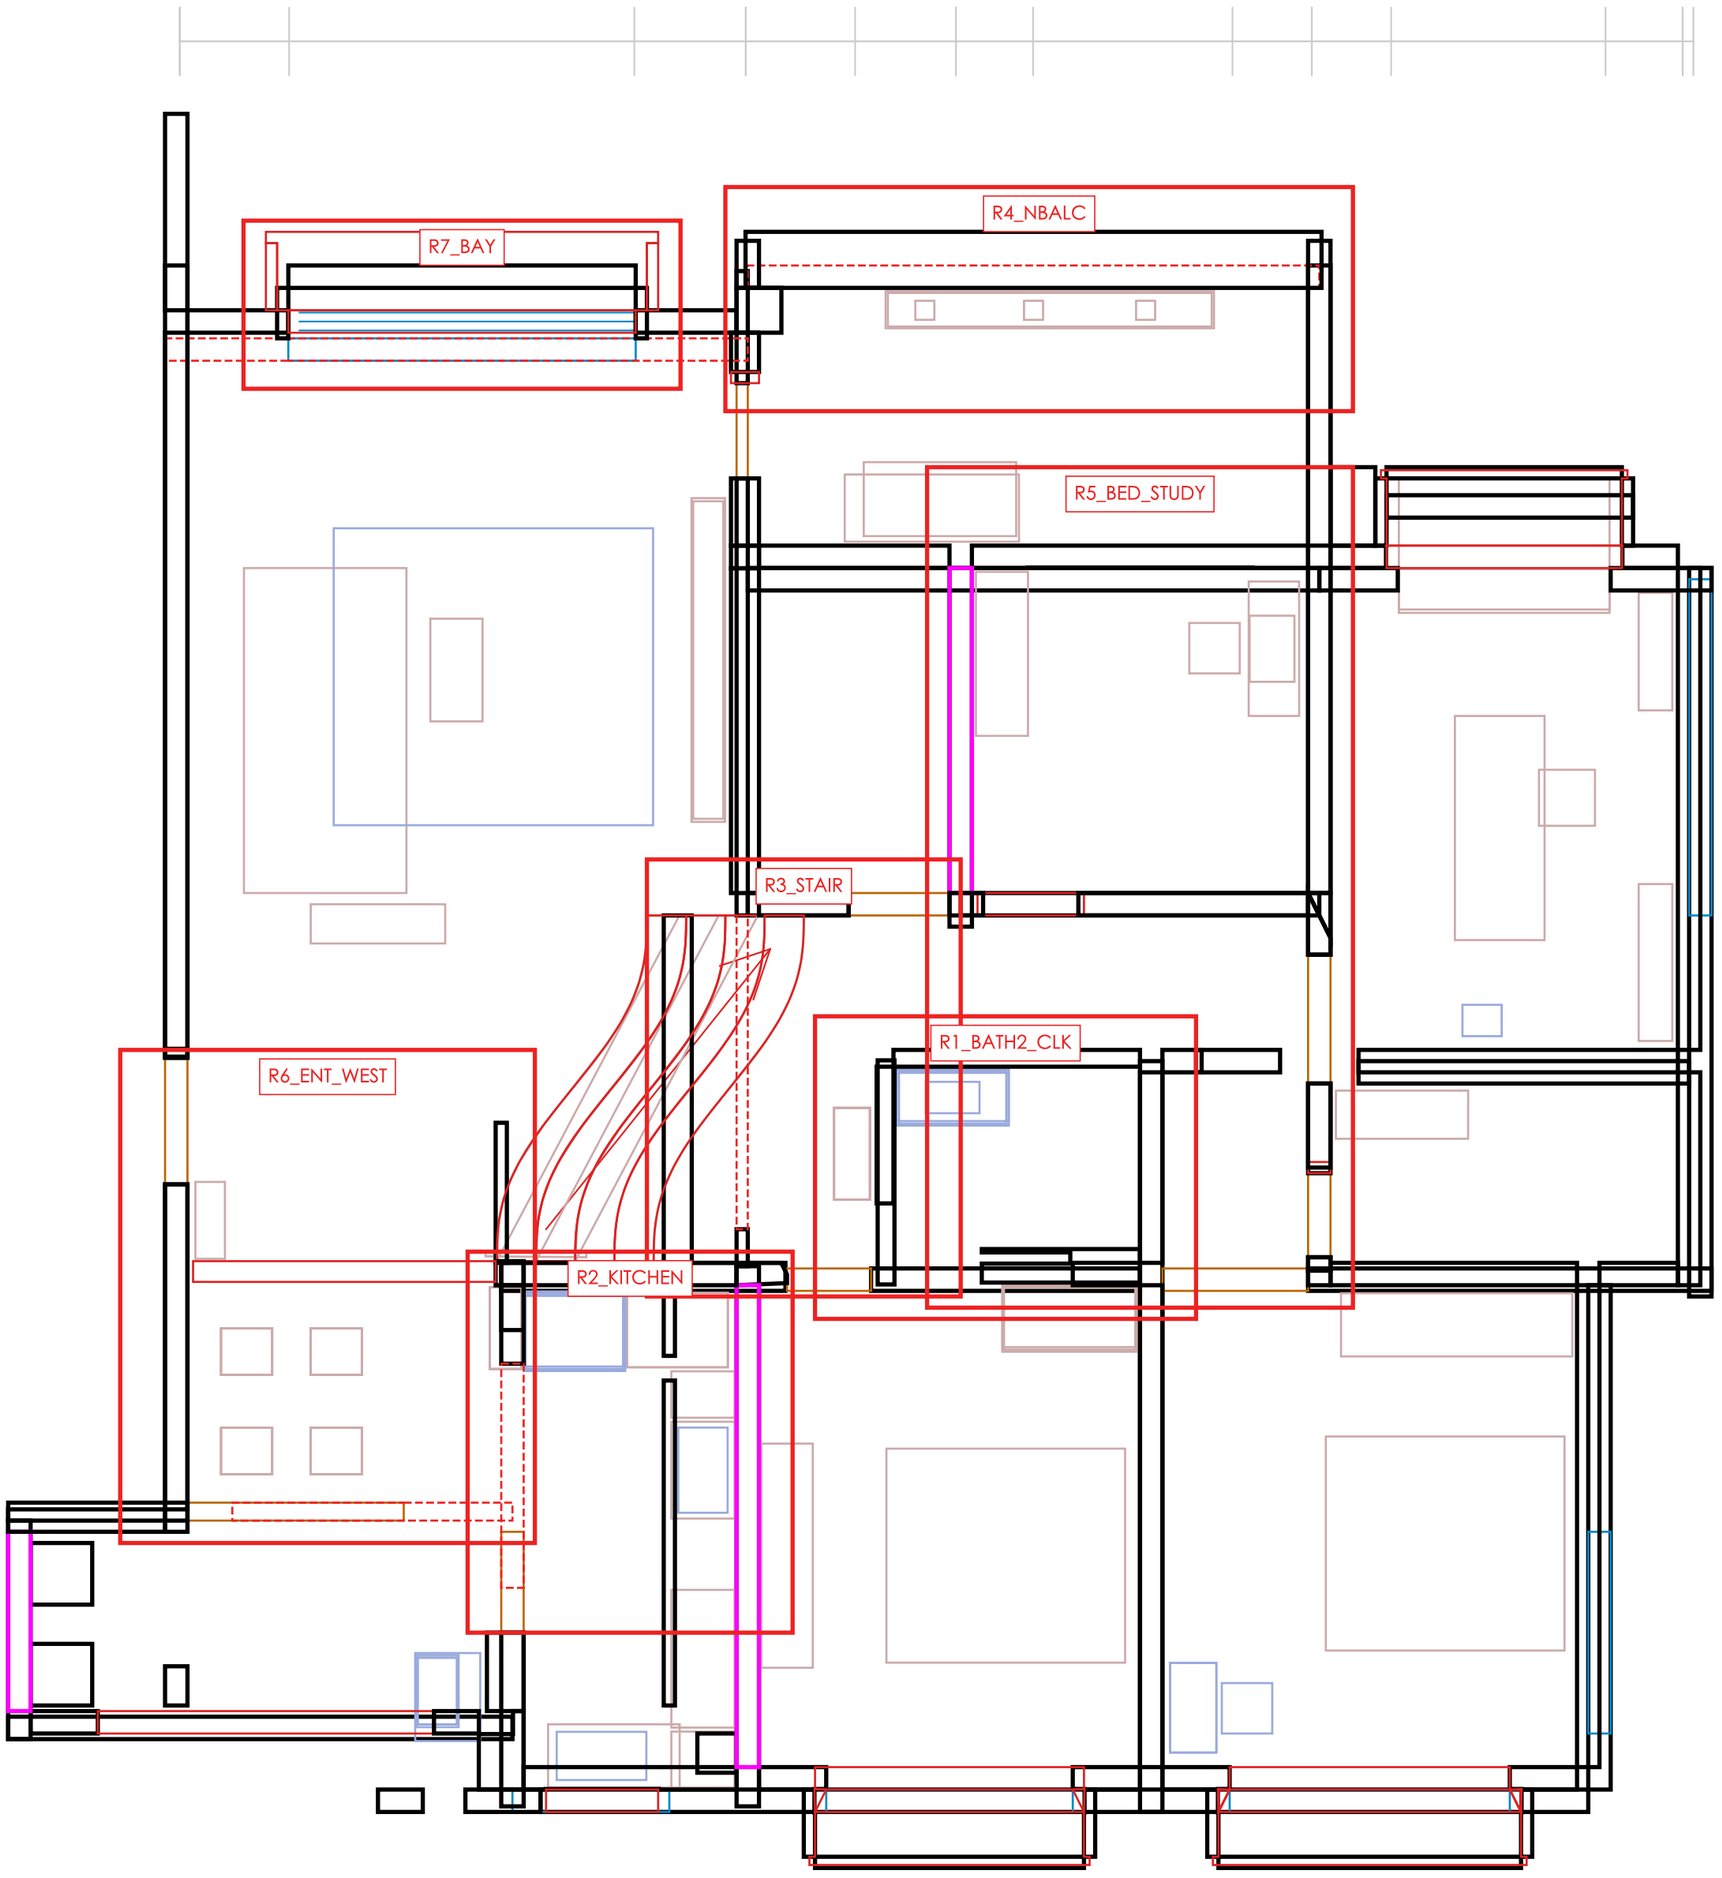
R7_BAY
R4_NBALC
R5_BED_STUDY
R3_STAIR
R6_ENT_WEST
R1_BATH2_CLK
R2_KITCHEN