
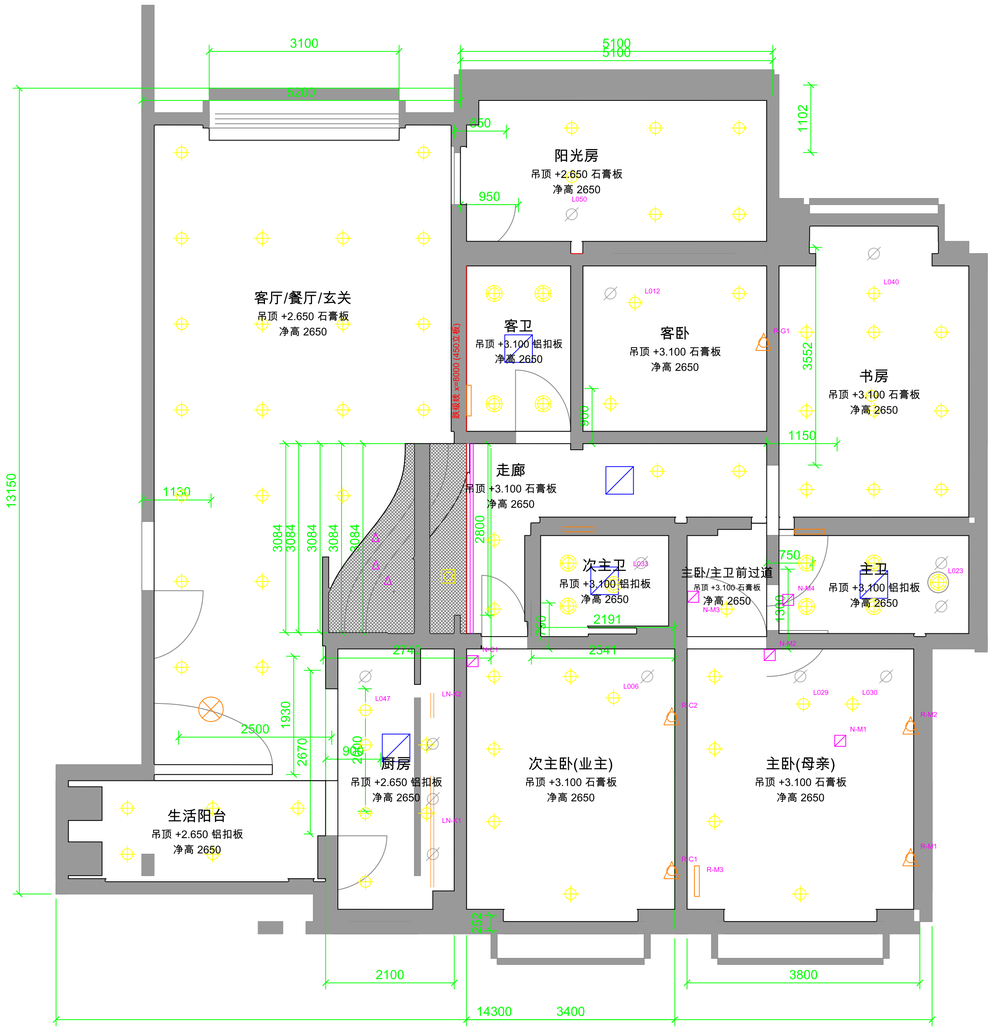


A201 V2 候选: 灯光优化 (FUNCTIONAL_DESIGN_REVIEW, 未经业主确认)

1. 基于 A201 V1 (94 点) 按房间审查: 保留 73、重新分组 8、移动 8、合并 1、取消 4、新增 13 -> 103 点
2. 移动原因: 衣柜/冰箱上柜/阳光房高柜/卧榻正上方, 次主卫淋浴区内
3. 厨房台面: 取消吊柜上方 3 盏, 改吊柜底灯带 (原灯被吊柜遮挡)
4. 母亲夜间路线: 床下感应 -> 门旁 -> 前过道 -> 主卫门内, 低位 3000K, 感应+定时
5. 新增床头阅读灯 5、梳妆镜前灯 1; 客厅/卧室电视墙与沙发墙单独调光
6. 灰色虚线 x 圈 = V1 原位置; 品红编号 = 新增/移动点
7. 未提供 IES/LDT 配光数据: 不判定照度、眩光达标; 淋浴区灯具分区由电气确认
8. 坐标与控制分组见 lighting_points_v2.json/csv; 正式 A201 未覆盖

□× 夜灯(低位)　○△ 床头阅读灯　═ 吊柜下灯带

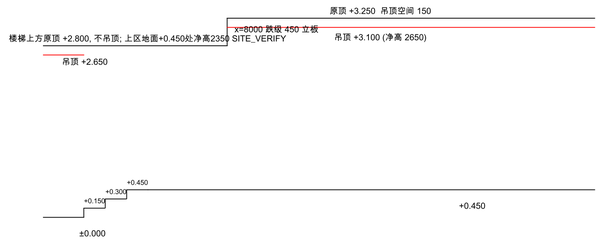

剖面示意 1-1 (y≈6000, 西→东), 1:50

A201 天花布置图 V2候选 (灯光优化, 未确认

图号 A201-V2　比例 1:50　图幅 A1　单位 mm

状态: 初步设计 PRELIMINARY_DESIGN - 非正式施工图, 尺寸须现场复核

源: A201_天花布置图_V2候选.dxf sha256:830a363cc7

出图: publish_dxf.py 2026-11-01