




BEFORE — bottom-left phantom L (parapet)

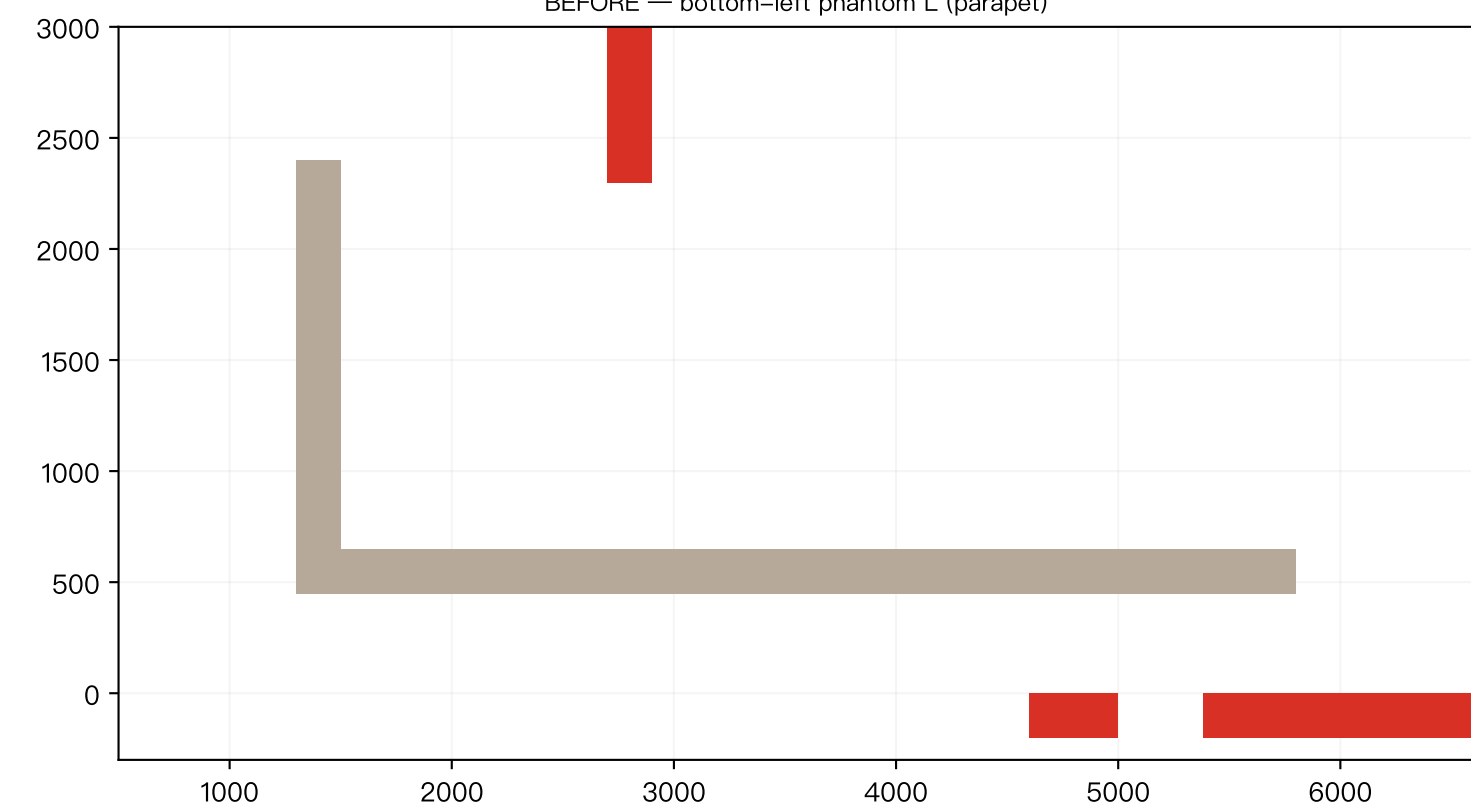


AFTER — bottom-left phantom L (parapet)

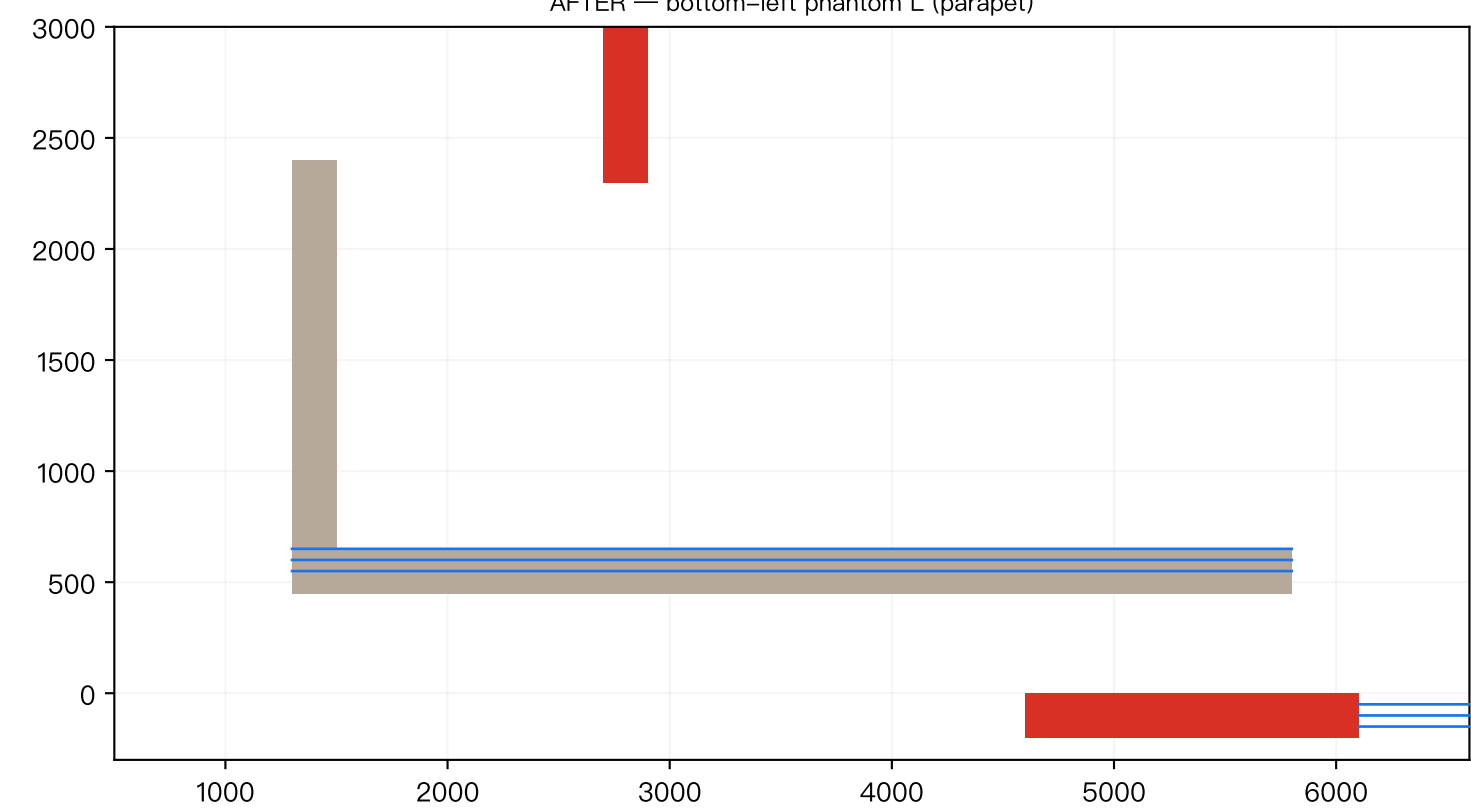


BEFORE — top floating red (living bay)

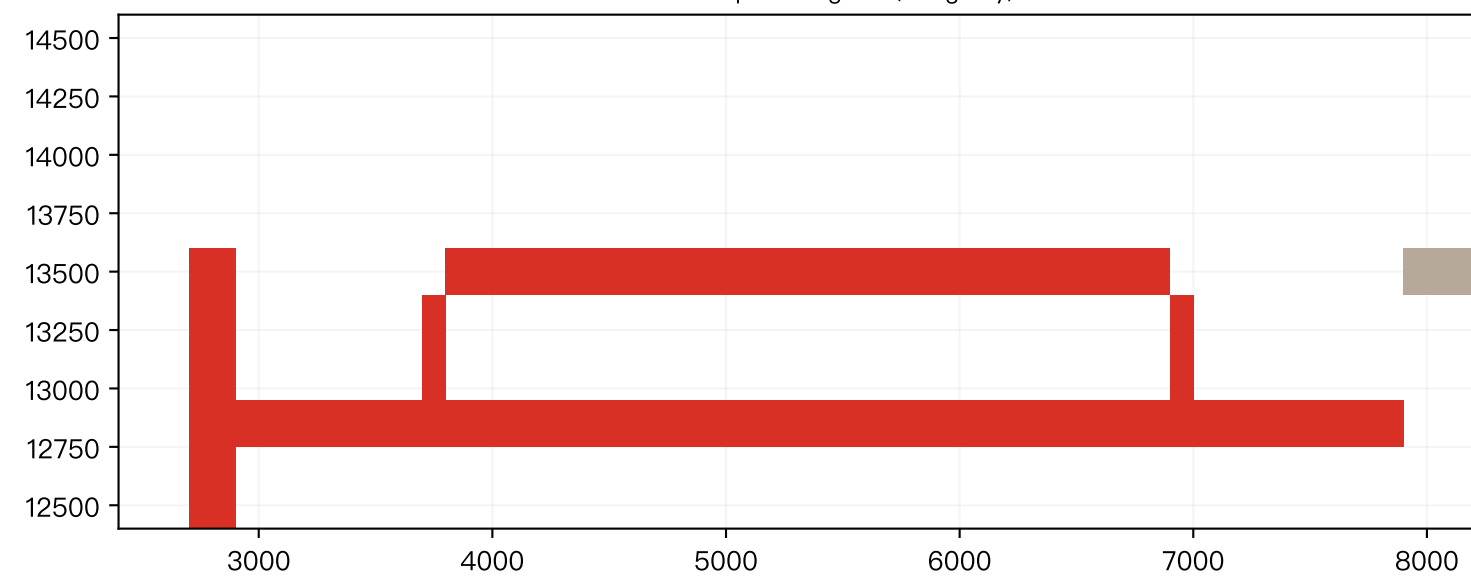


AFTER — top floating red (living bay)

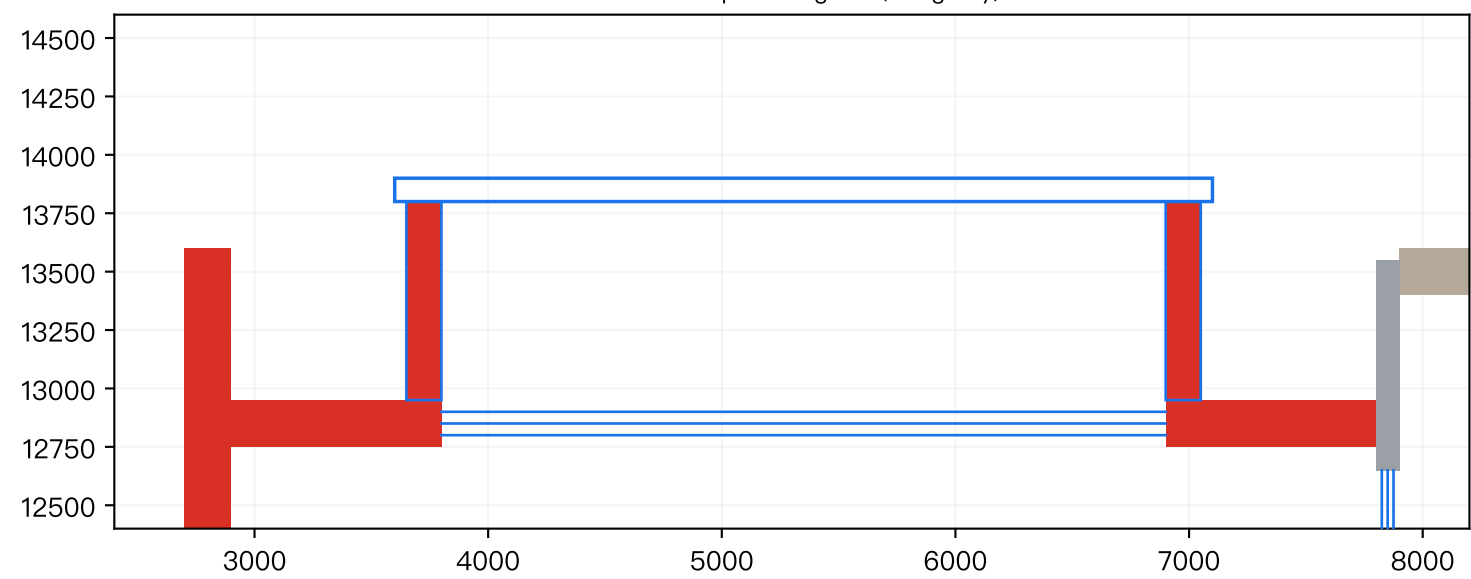


BEFORE — right floating red (study NE bay)

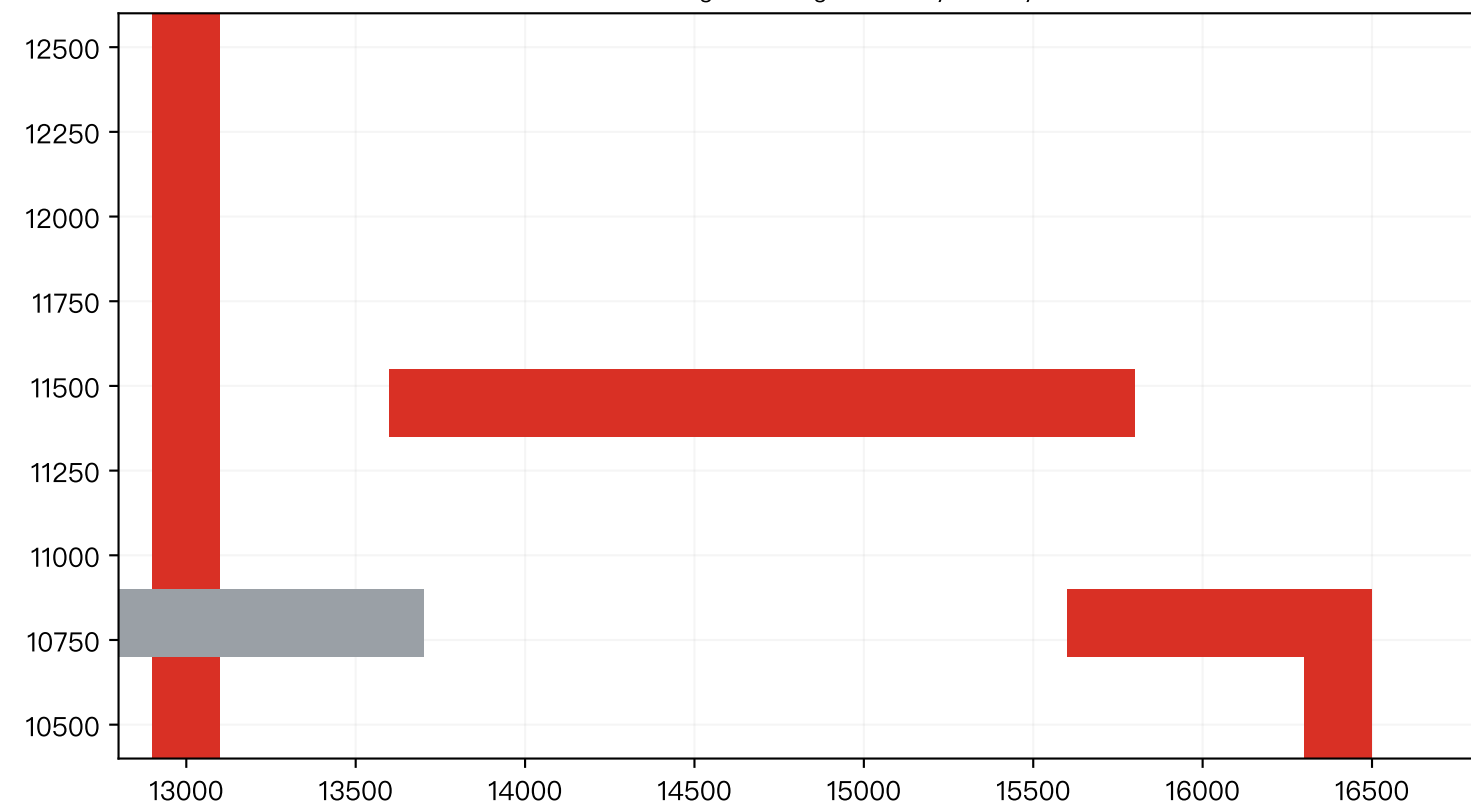

AFTER — right floating red (study NE bay)

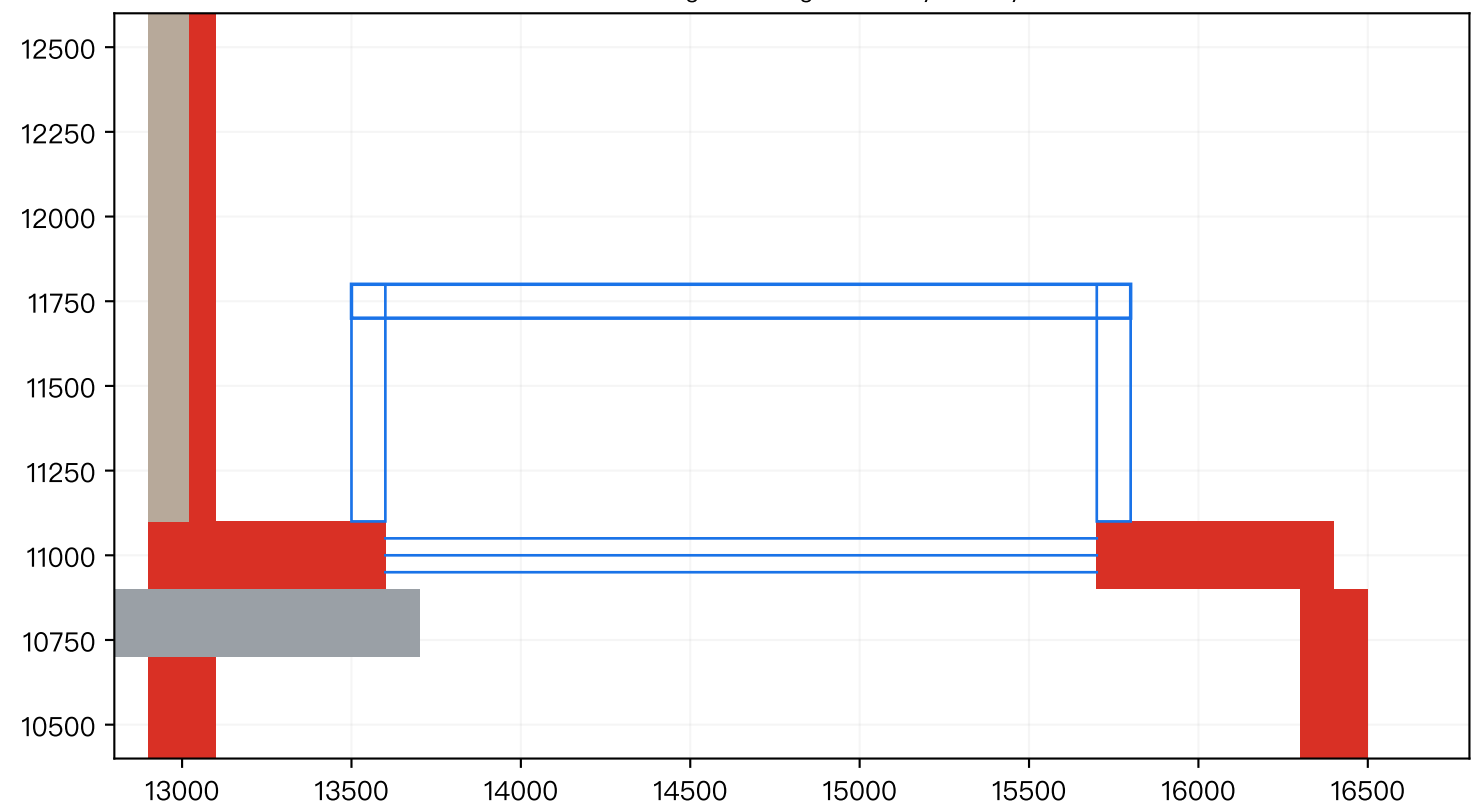

BEFORE — south windows

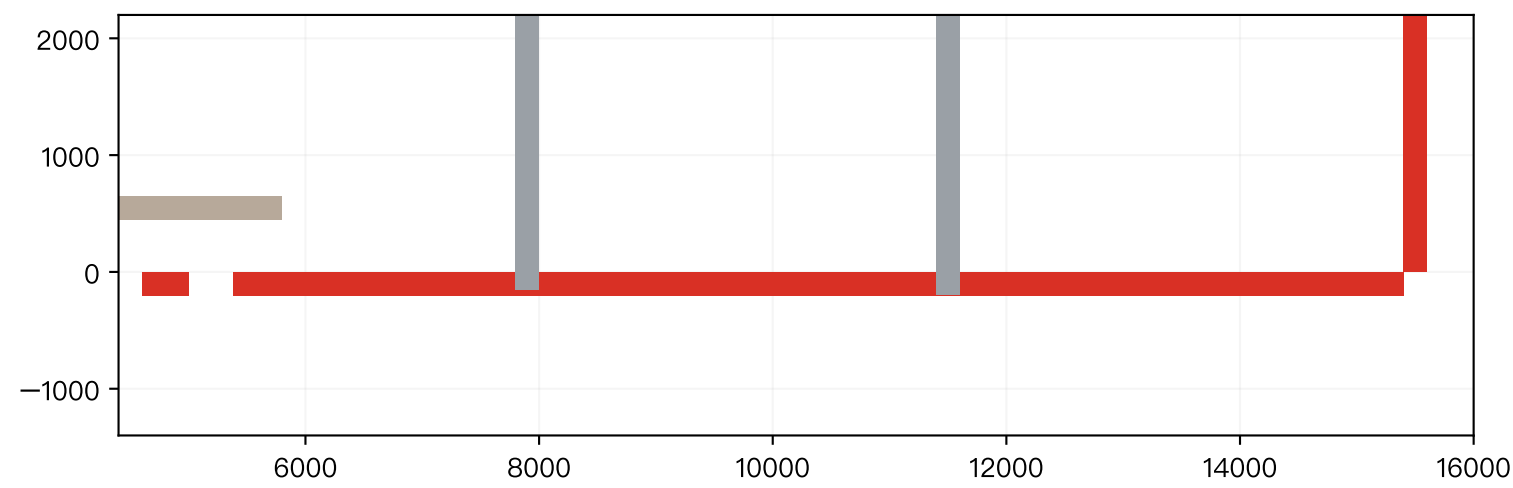

AFTER — south windows

