

PROJECT NAME
项 目 名 称

AREA&FLOOR
区域 & 楼层

PRODUCT TITLE
品 名 称

DWG. NO.
图 纸 编 号
图 纸 编 号

VERSION NO.
图 纸 版 本 号
成都

DATE
紙 期
2024-08-31

Page No. _____
页 码 _____

DESIGN
设计
9楼

CHK BY
审核

CHD BY
校 对


CLIENT CHK
客户确认

UNIT
单位
mm

NOTE	第三级
------	---

第三视角

△ 分拆标志

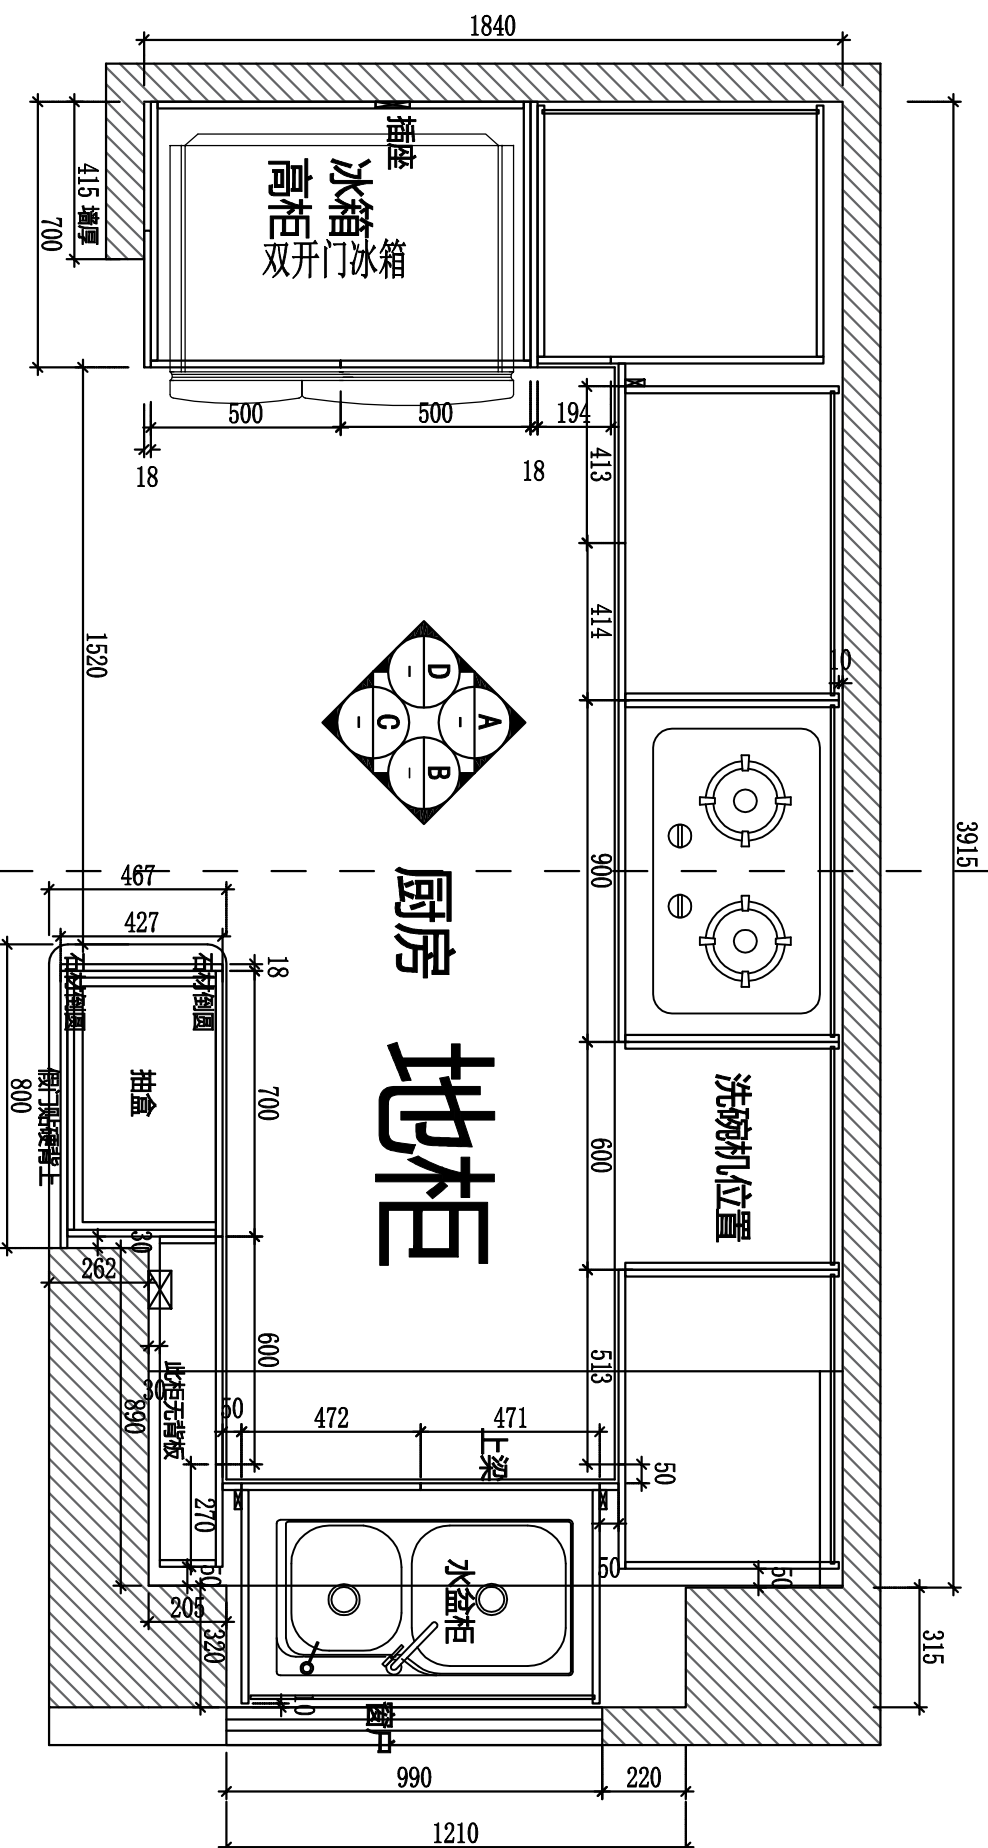

方 案 圖

PROJECT NAME	世纪欣园3-1-901#
项目名称	
AREA/FLOOR	区 楼 & 梯 户

9楼

PRODUCT TITLE
品 名 称

DWG NO.
图 纸 编 号
图纸编号

VERSION NO.
图 纸 版 本 号
成都

DWG DATE
图 纸 日 期
2024-08-31



页码

计 9楼


CHK BY 核 审

CHD BY 校 対

客户确认	
UNIT 单位	mm
NOTE	A3版面
 代表必须  代表建议  分析确定	 第三视角 发放图样编号与序号

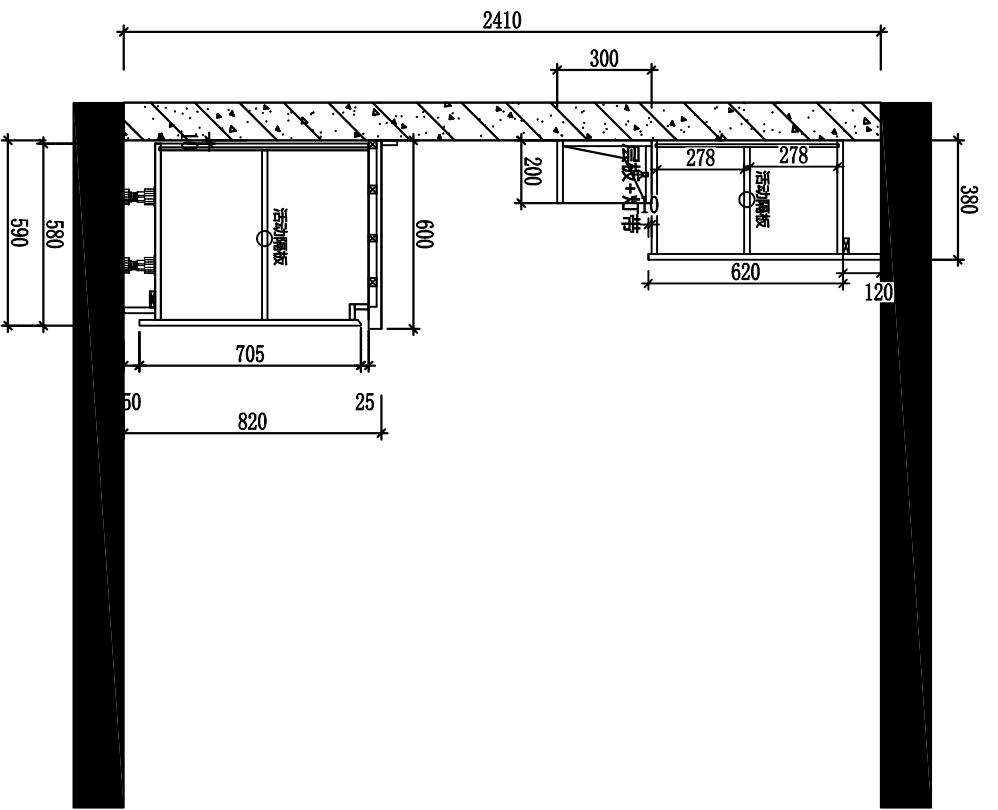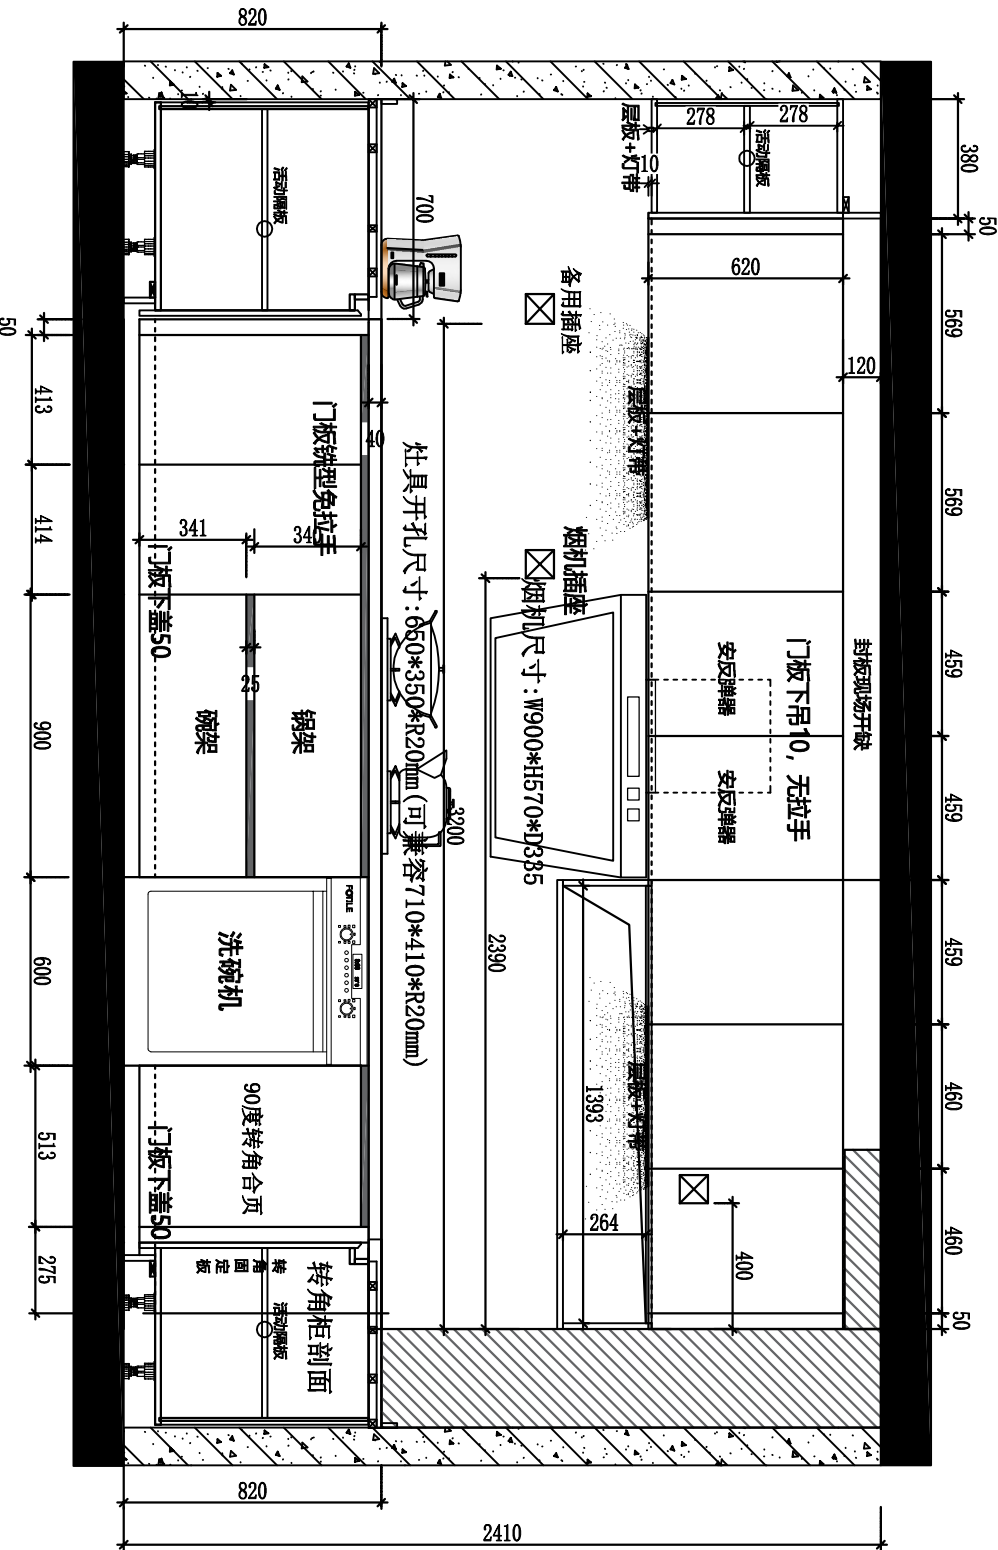

立面图
比例1:1

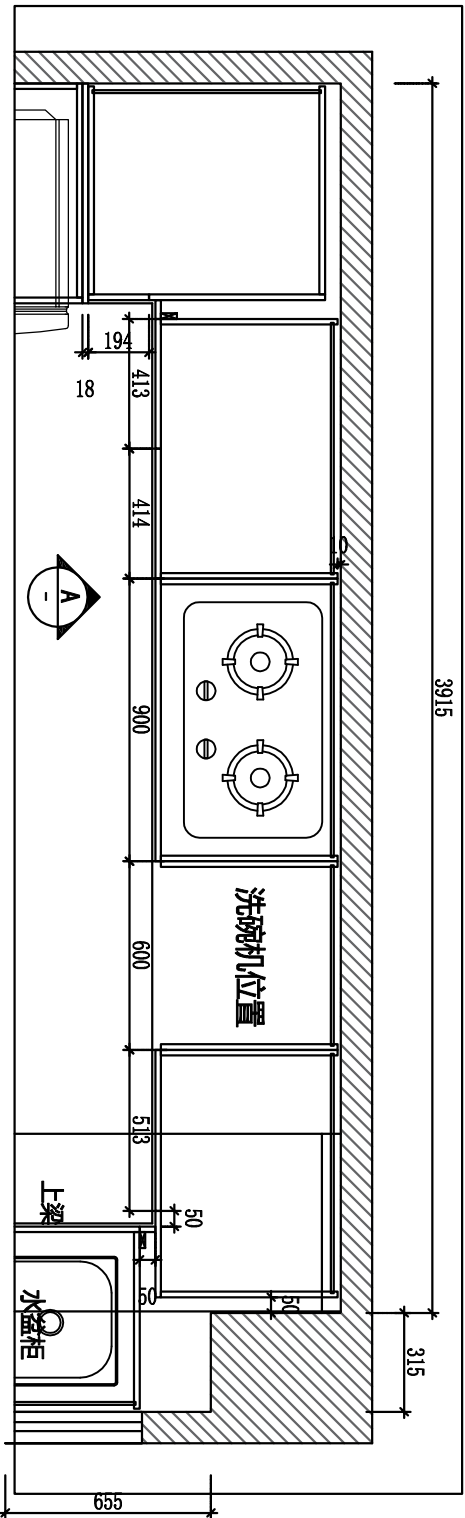


柜体：布拉格（拉米系列），实木颗粒板

门板+看面板+收口条: SM962002范托尼柚木 (日本住友, F4星)

石材：赫拉白

灯带: 4000K中性光??, 触摸式开关(注意: 延长线多配点, 分线盒, 变压器配够)

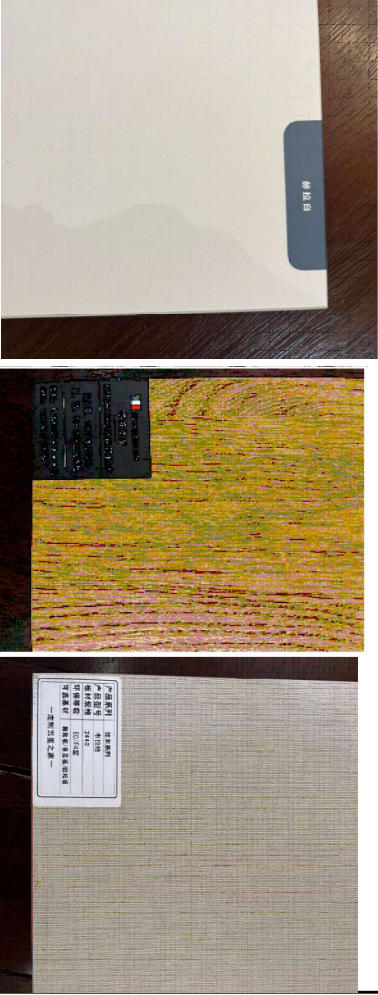

方案案图

PROJECT NAME
项目名称

世纪欣园3-1-901#

AREA&FLOOR
区域 & 楼层

9楼

PRODUCT TITLE
产品名称
橱柜

DWG NO.
图纸编号
图纸编号

VERSION NO.
图纸版本号
成都

DWG DATE
图纸日期
2024-08-31

Page No.
页码
页码

DESIGN
设计
9楼

CHK BY
审核

CHD BY
校对

CLIENT CHK
客户确认

UNIT
单位
mm


A3版面

NOTE
代建见光面


第三视角

分栋标注

发放图纸编号序号

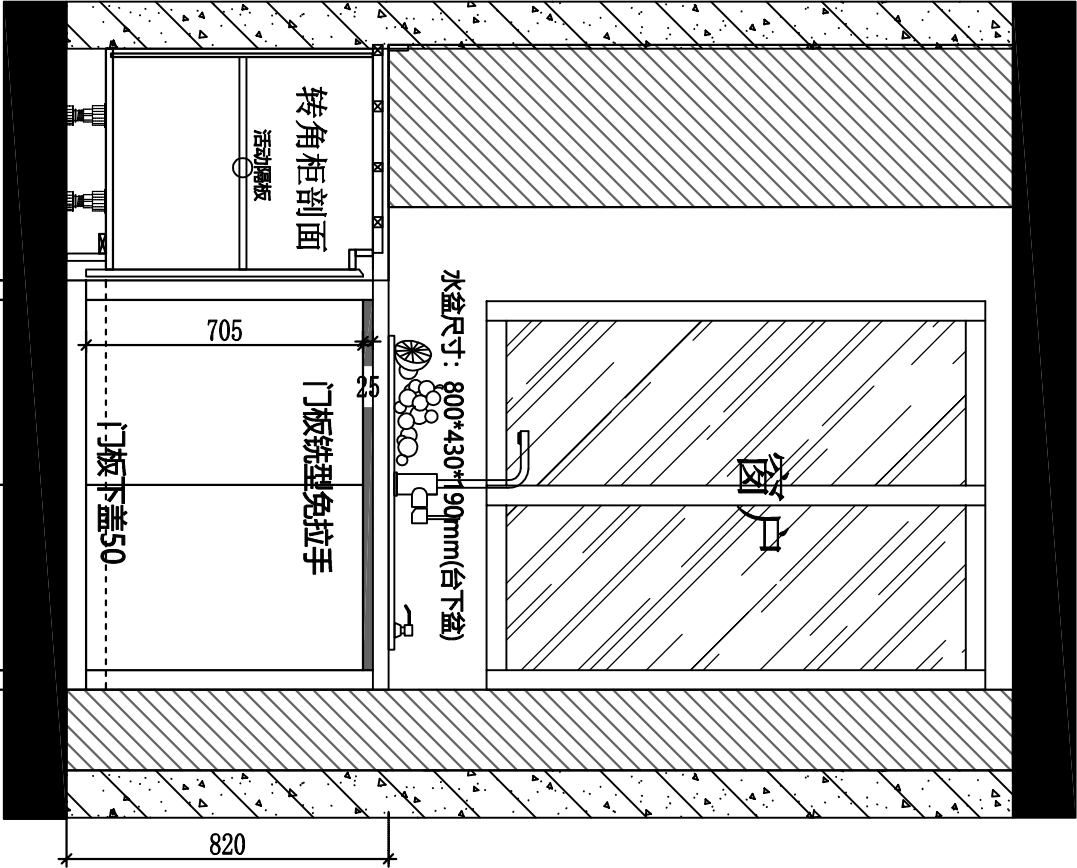

立面图
比例1:1

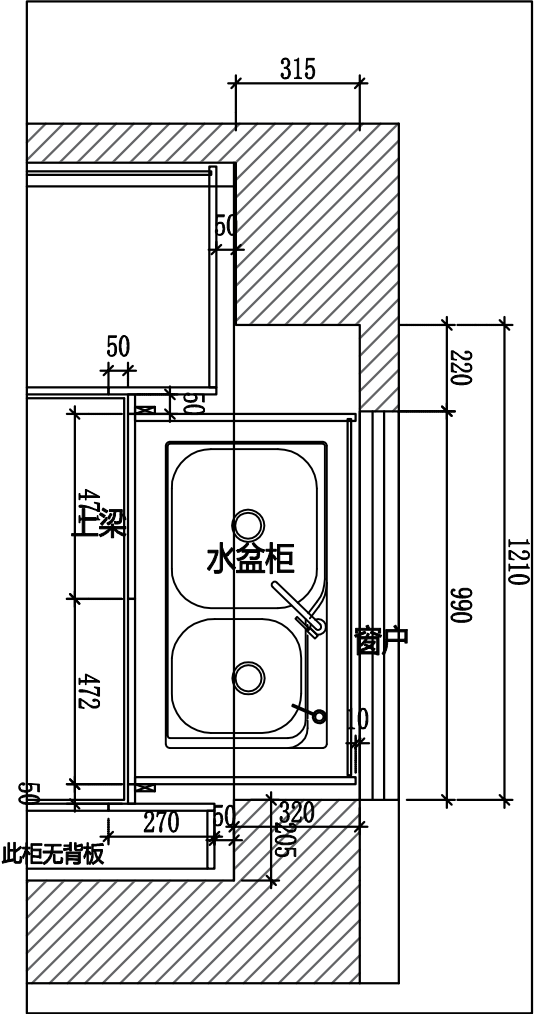


柜体：布拉格（拉米系列），实木颗粒板
门板+看面板+收口条:SM962002范托尼柚木（日本住友，F4星）
石材：赫拉白


产品型号	材质	工艺	表面处理	安装环境	备注
文粹300单槽	304不锈钢	一体拉伸	拉丝	台上/台下/台下	圆形开孔式




水槽详细尺寸图参考
(SK42811C)

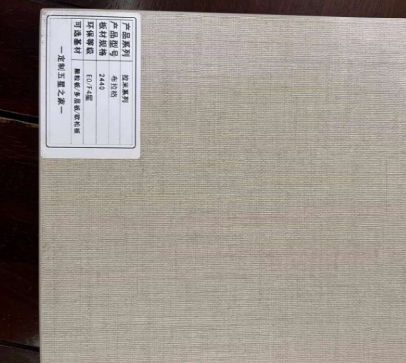


方案图

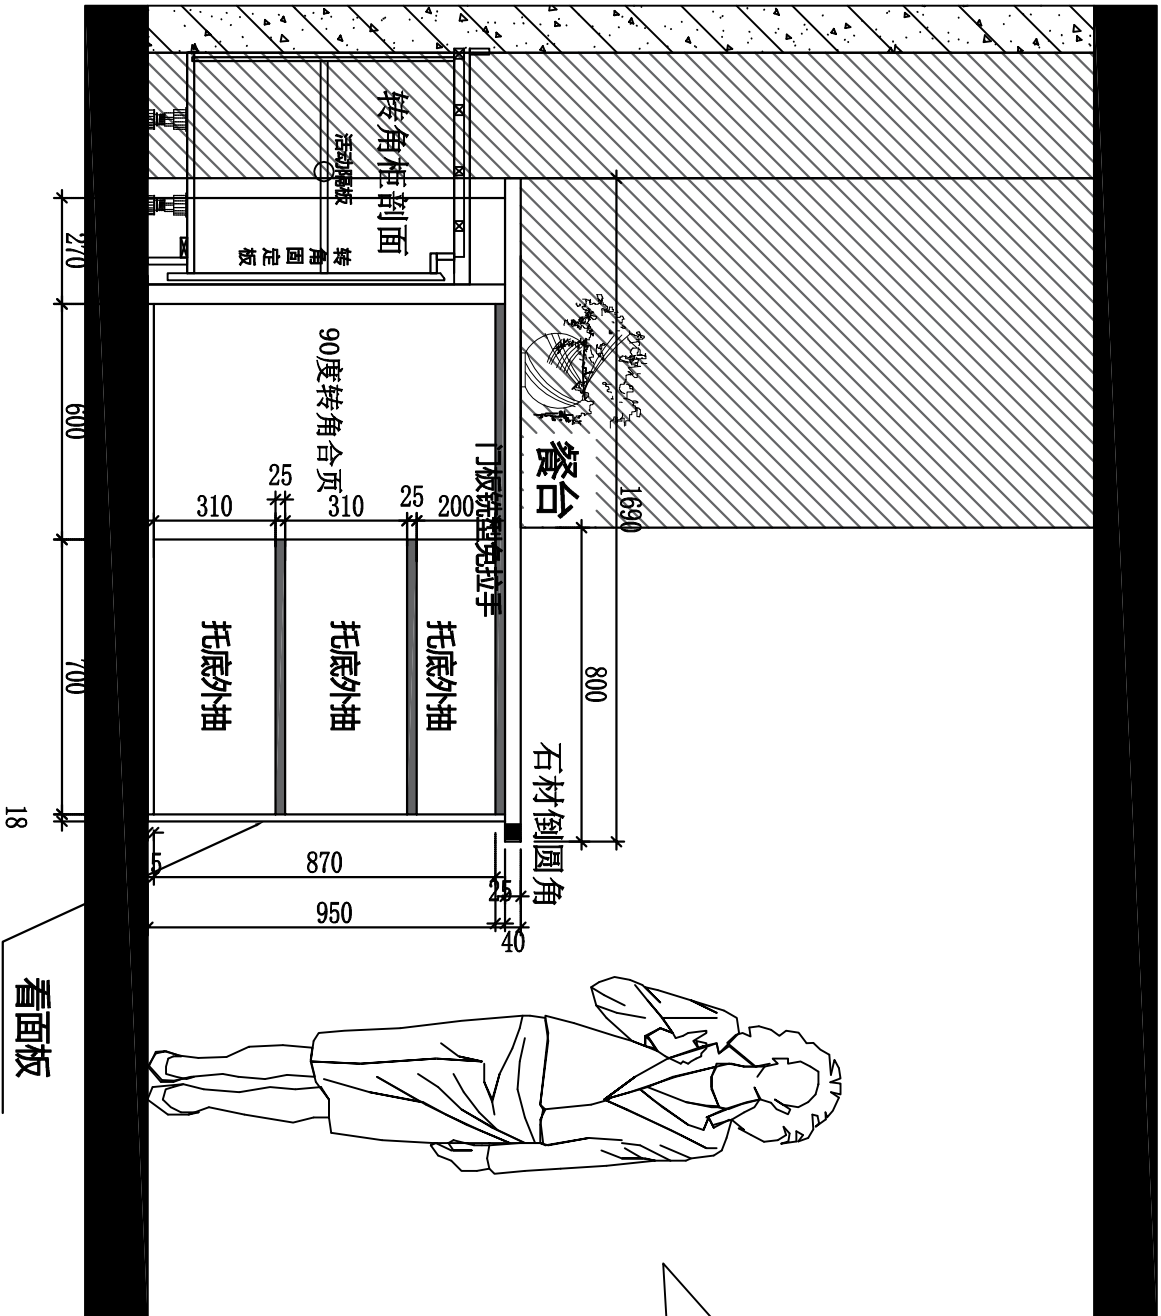

立面图
比例1:1

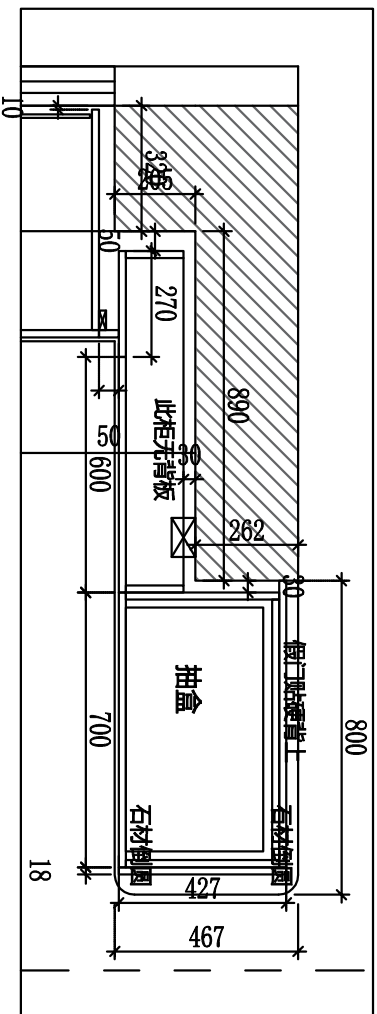


柜体：布拉格（拉米系列），实木颗粒板
门板+看面板+收口条：SM962002范托尼柚木（日本住友，F4星）
石材：赫拉白

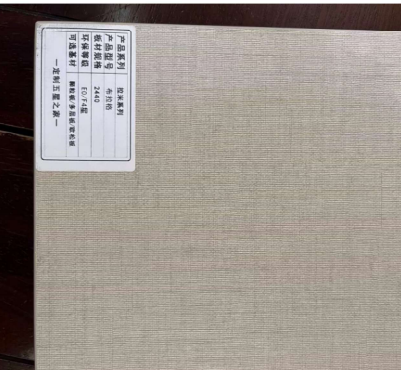


PROJECT NAME 项 目 名 称		世纪欣园3-1-901#		
AREA&FLOOR 区 域 & 楼 层		9楼		
PRODUCT TITLE 产 品 名 称		橱柜		
DWG. NO. 图 纸 编 号				
VERSION NO. 图 纸 版 本 号				
DWG. DATE 图 纸 日 期				
Page No. 页 码				
DESIGN 设 计				
CHK BY 审 核				
CHD BY 校 对				
CLIENT CHK 客 户 确 认				
UNIT 单 位	mm	A3版面		
NOTE 代建/代建/代建	第三视角			
分拆标注	发放图纸编号/序号			

方案图

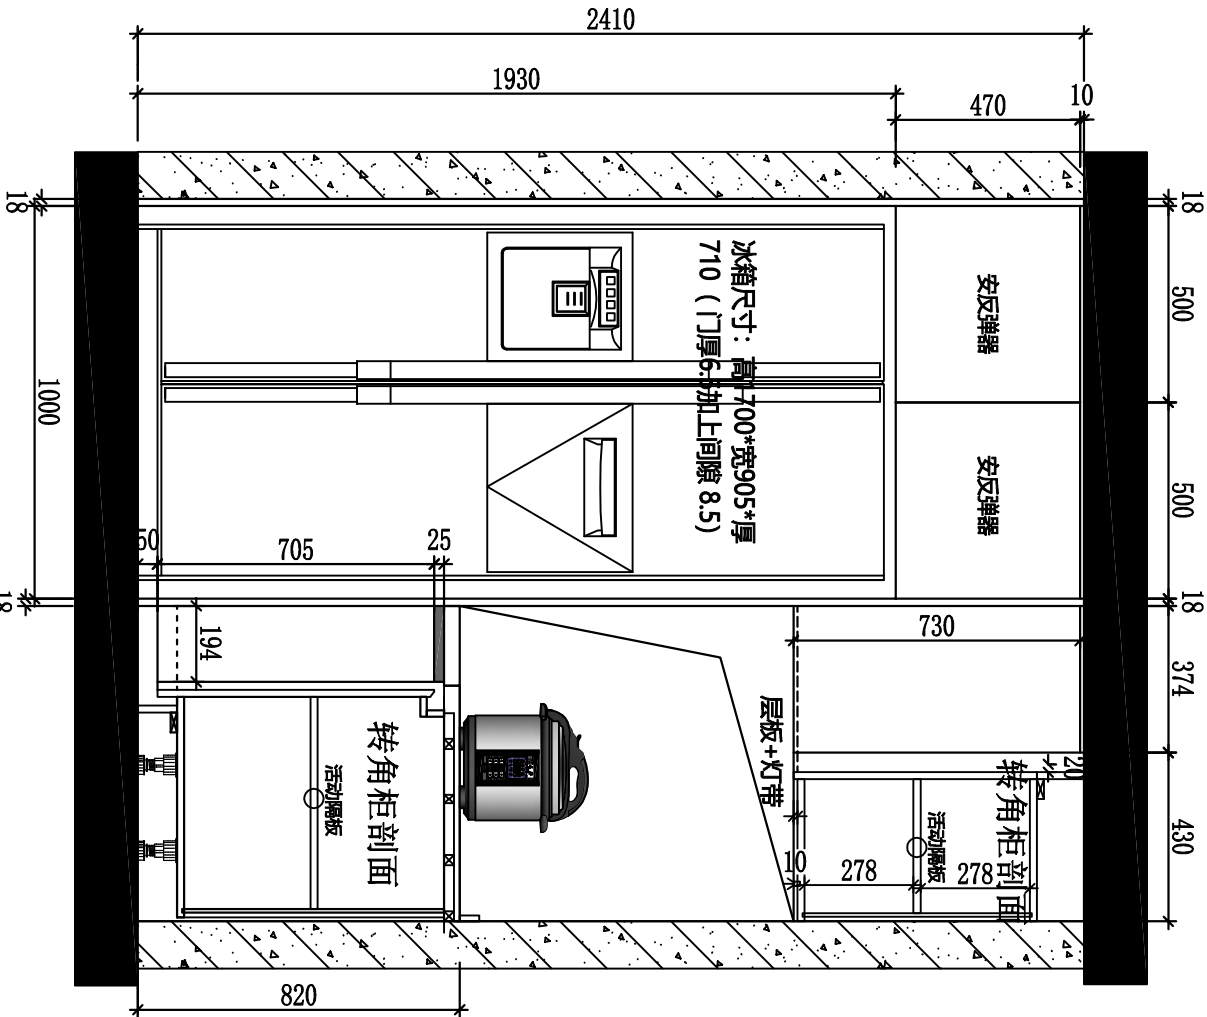

立面图
比例1:1

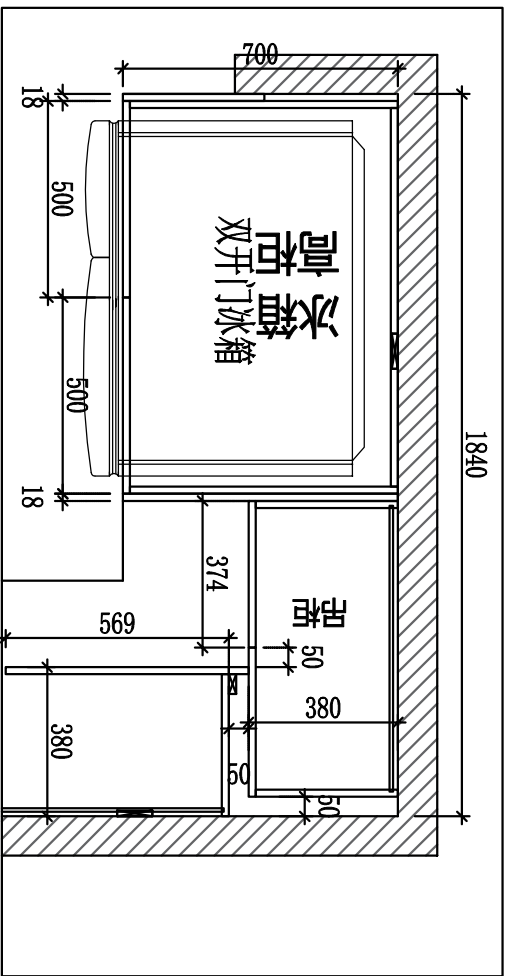

冰箱尺寸: 高1700*宽905*厚710 (门厚6.5加上间隙 8.5)

柜体: 布拉格 (拉米系列), 实木颗粒板
门板+看面板+收口条: SM962002范托尼柚木 (日本住友, F4星)
石材: 赫拉白
灯带: 4000K中性光??, 触摸式开关(注意: 延长线多配点, 分线盒, 变压器配够)

PROJECT NAME 项 目 名 称		世纪欣园3-1-901#	
AREA&FLOOR 区 域 & 楼 层		9楼	
PRODUCT TITLE 产 品 名 称		橱柜	
DWG NO. 图 纸 编 号	图纸编号		
VERSION NO. 图 纸 版 本 号	成都		
DWG DATE 图 纸 日 期	2024-08-31		
Page No. 页 码	9楼		
DESIGN 设 计	9楼		
CHK BY 审 核			
CHD BY 校 对			
CLIENT CHK 客 户 确 认			
UNIT 单 位	mm	A3版面	
NOTE 代建/代建/代建/分拆标注	第三视角 发版图纸编号/序号		



方案图

PROJECT NAME
项目名称

世纪欣园3-1-901#

AREA&FLOOR
区域&楼层

9楼

PRODUCT TITLE
产品名称
餐厅阳台储物柜

DWG NO.
图纸编号
图纸编号

VERSION NO.
图纸版本号
成都

DWG DATE
图纸日期
2024-08-31

Page No.
页码
页码

DESIGN
设计
9楼

CHK BY
审核



CHD BY
校对

CLIENT CHK
客户确认

UNIT
单位
mm

A3版面

NOTE	代建见光面	第三视角
▲	代建见光面	分拆标注

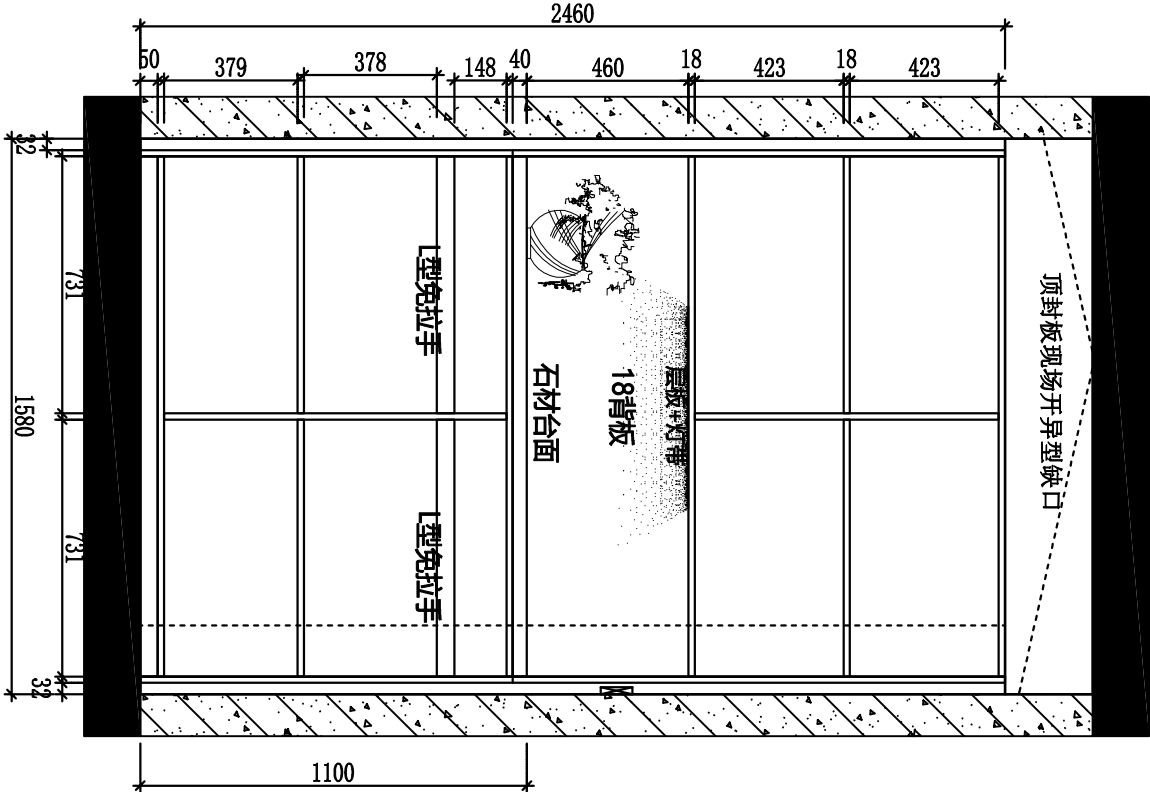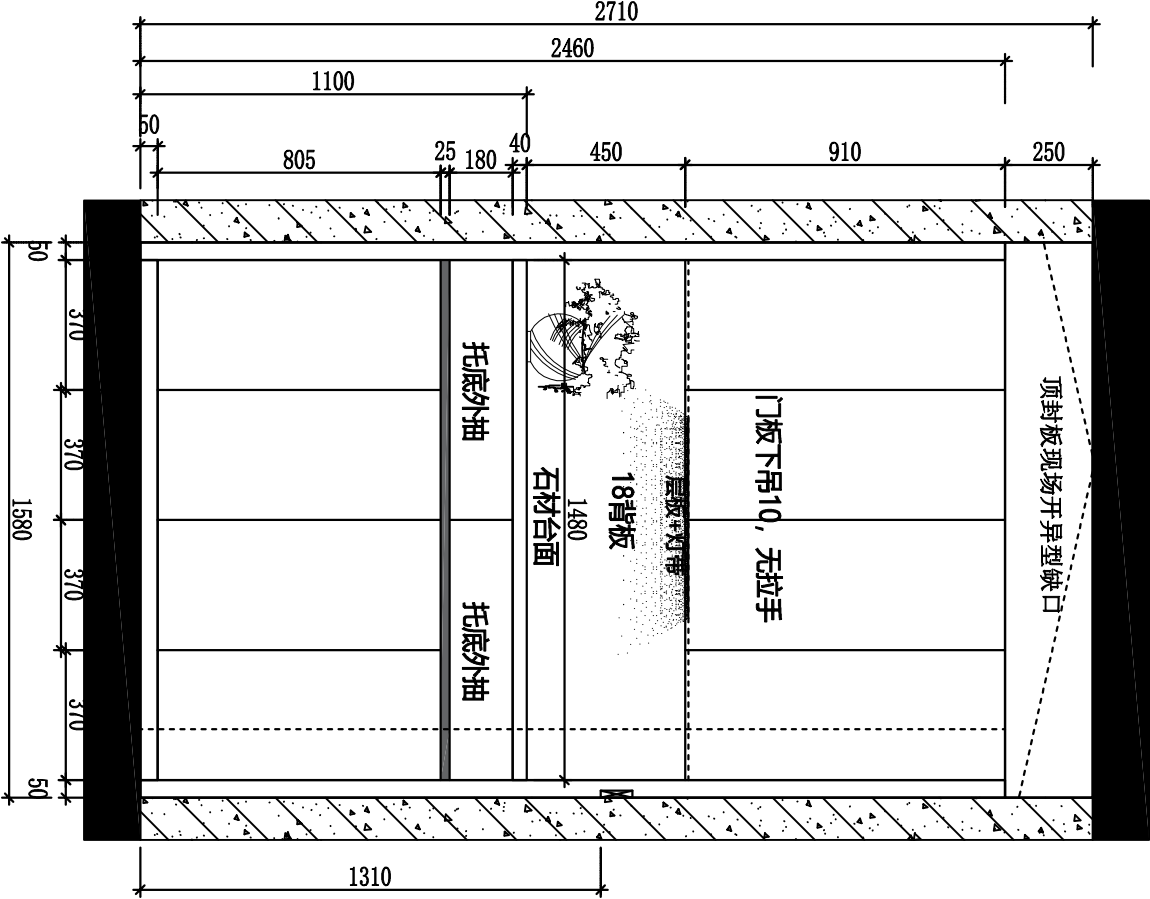

柜体：布拉格（拉米系列），实木颗粒板
门板+看面板+收口条：SM962002范托尼柚木（日本住友，F4星）
石材：赫拉白

