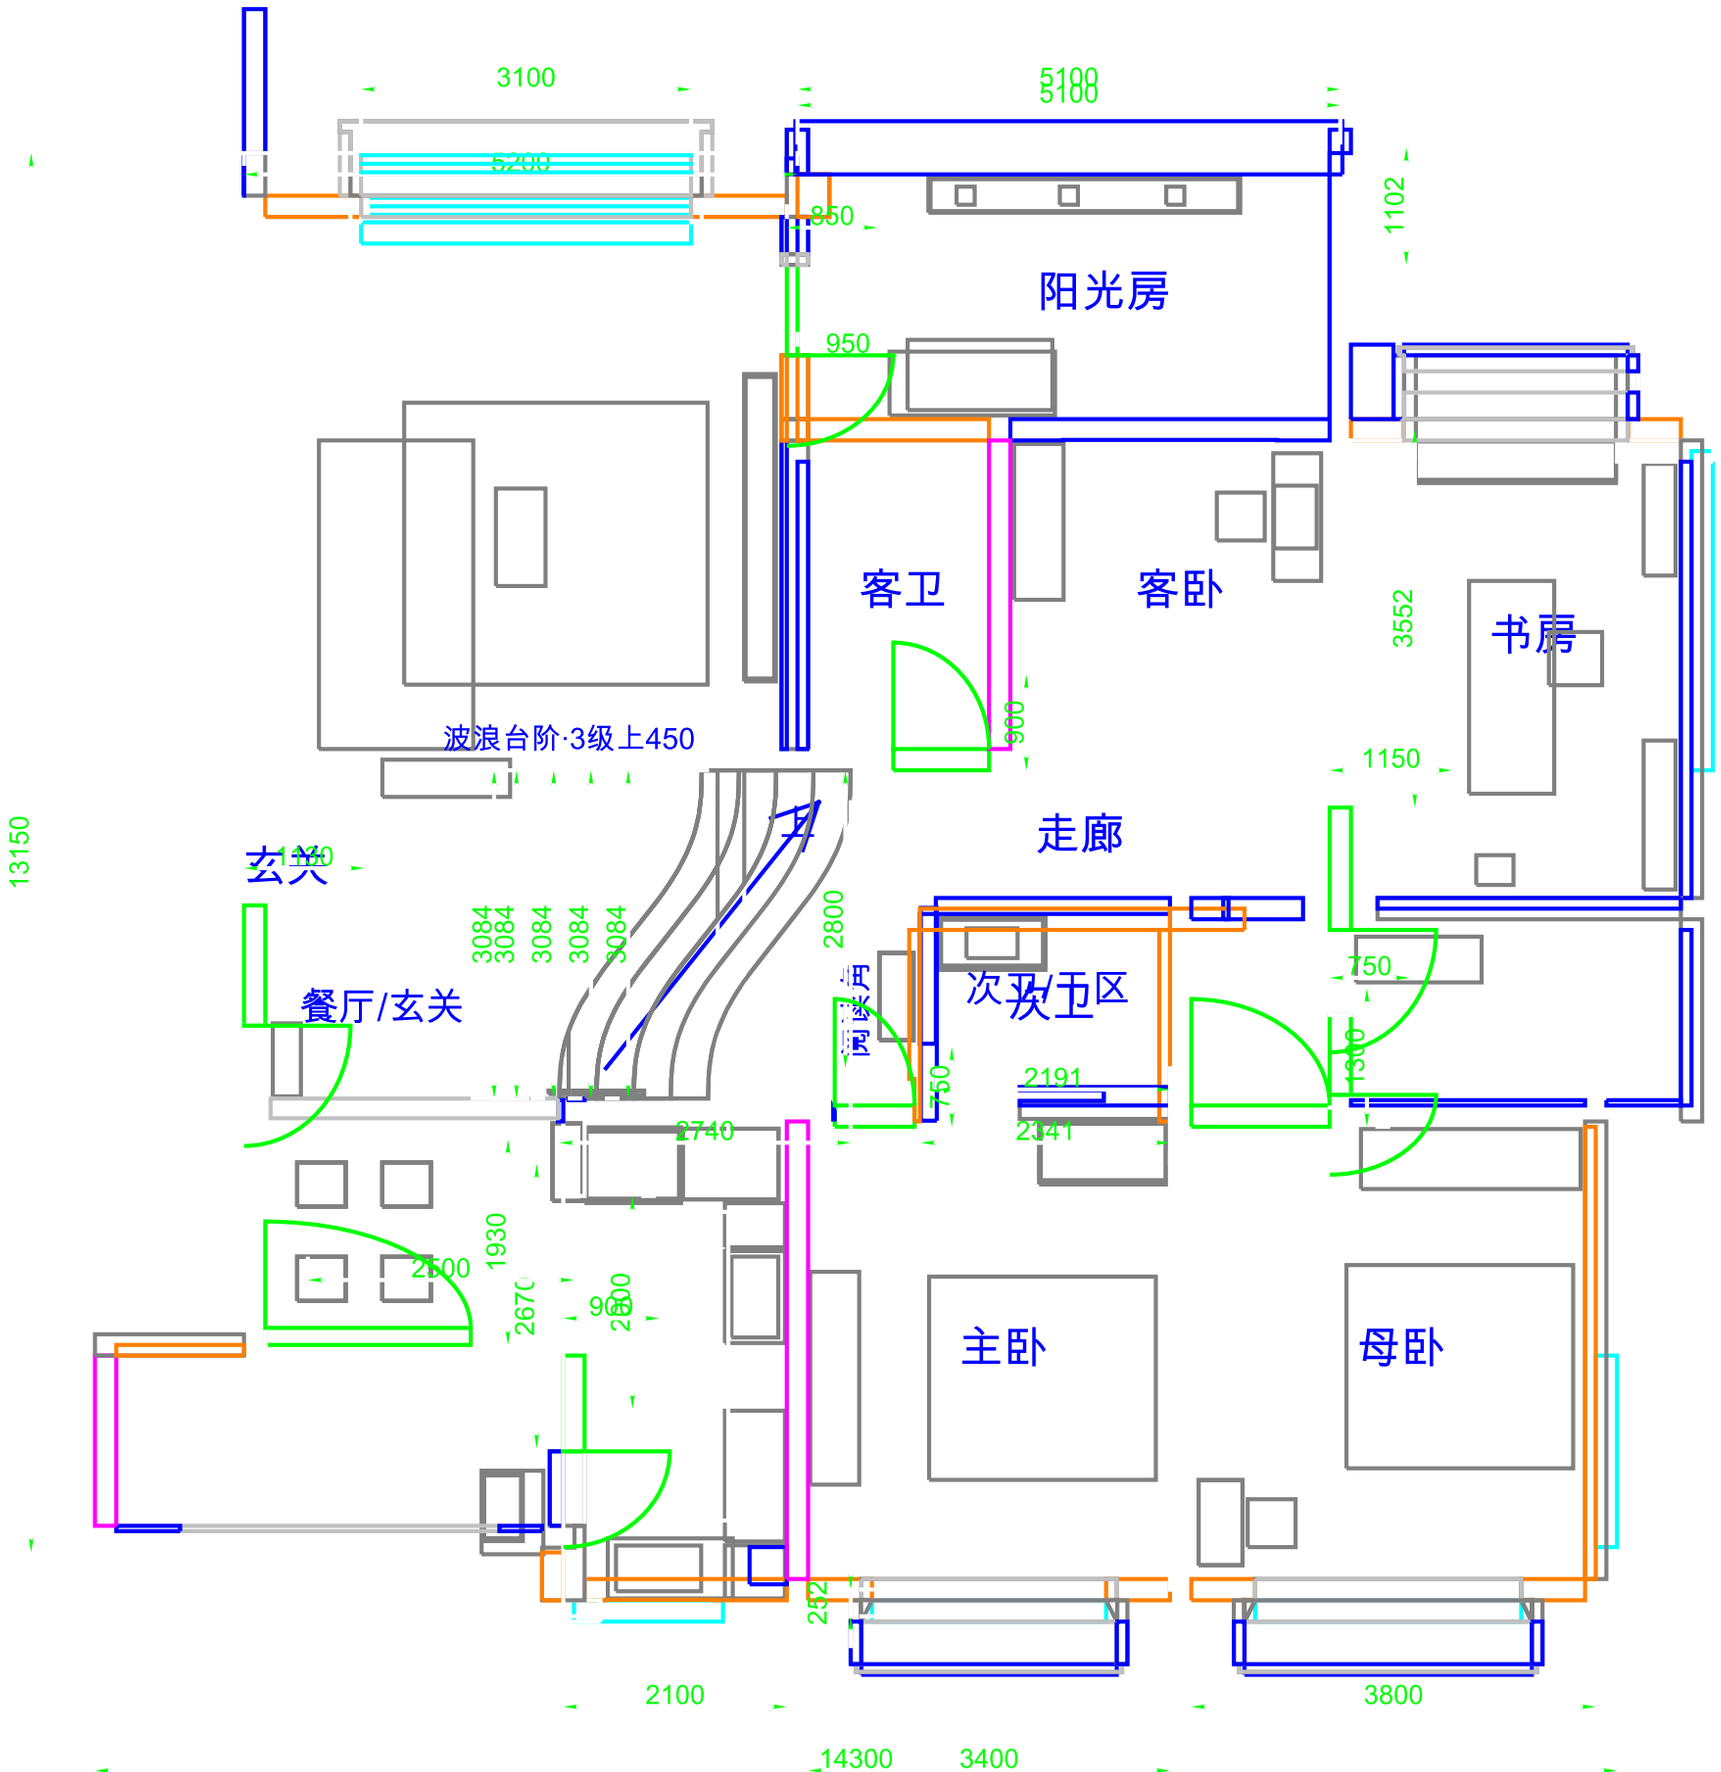

3100
5100
5100
5200
850
1102
阳光房
950
客卫
客卧
3552
书房
900
波浪台阶·3级上450
1150
走廊
13150
玄关
3084
3084
3084
3084
3084
2800
餐厅/玄关
次卫/干区
750
1300
2191
2341
750
2740
1930
2500
2670
900
2800
主卧
母卧
252
2100
3800
14300
3400