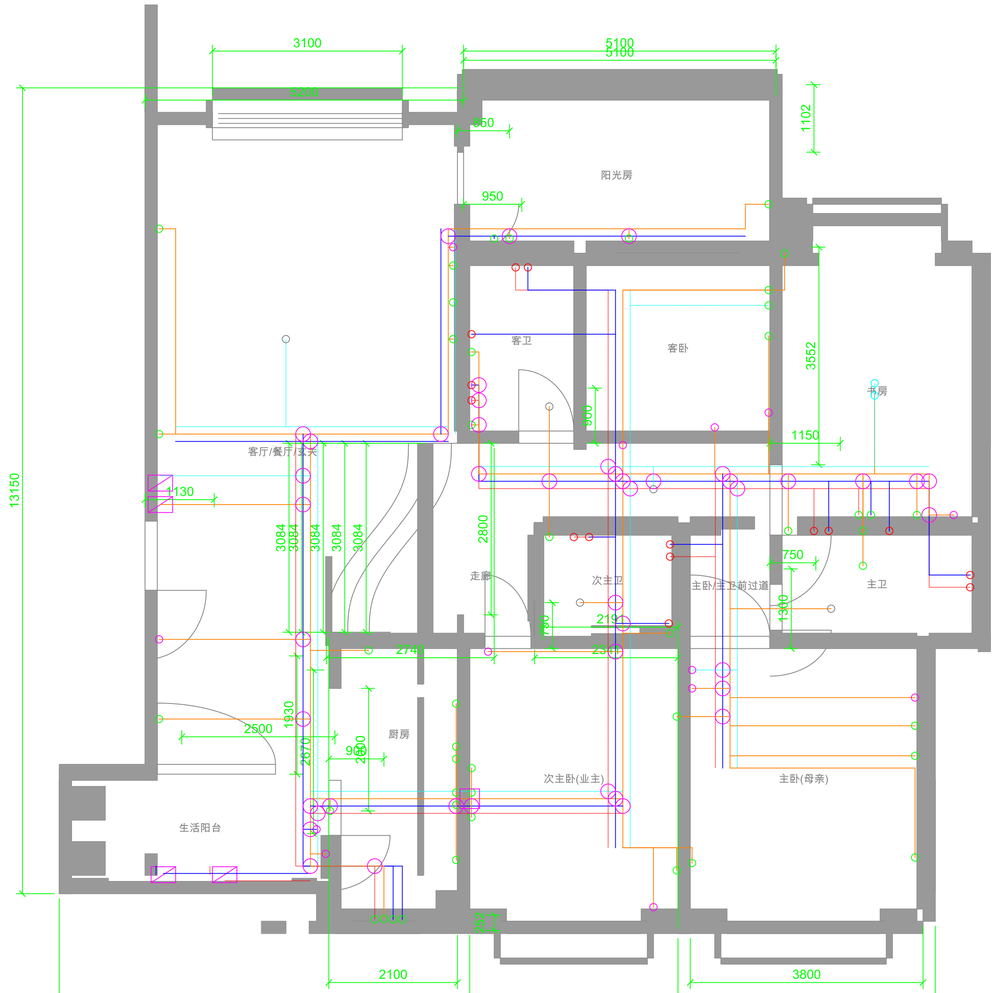


A301 吊顶内管线路由示意 1:50 CD_V01 SCHEMATIC / SITE_VERIFY_REQUIRED

A301 吊顶内管线路由示意 (CD_V01, 示意, 非施工定案)

1. 强电/弱电/冷水/热水均走吊顶内, 不在墙面开槽; 线位为示意, 未定管径与根数
2. 吊顶下返 150: 吊顶内净空、龙骨、梁位未实测 -> SITE_VERIFY_REQUIRED, 不代表管线可全部装下
3. 配电箱/弱电箱/给水入户/热水器位置未知, 圈中品红框为 TBD 占位
4. 水管在下、电线在上; 品红圆圈 = 水电交叉点, 需保持间距或套管 (由施工方定)
5. 品红方框 = 穿越 2650/3100 吊顶高差 (x=8000 电视墙) 处, 需开孔或绕行, 结构许可待定
6. 楼梯区与 x<8000 上区地面为原顶无吊顶, 管线不经过
7. 竖向下引: 绿=浴家具/柜体背板; 红=卫浴假墙/包管 TBD; 青=地面垫层 TBD; 灰=吊顶内设备; 品红=隔墙空腔/明装线槽 TBD
8. 排水: 业主自行处理, OUT_OF_SCOPE, 本图不表达
9. 物理回路、开关接线、灯带驱动均为 TBD; 详见 A302

- 强电 (实线)
- 弱电/网络 (虚线)
- 冷水 (实线)
- 热水 (虚线)

A301 吊顶内管线路由示意 (示意, 非施工定案

图号 A301　比例 1:50　图幅 A1　单位 mm

状态: 初步设计 PRELIMINARY_DESIGN - 非正式施工图, 尺寸须现场复核

源: A301_吊顶管线路由示意.dxf sha256:cb04379d2e

出图: publish_dxf.py 2026-11-01