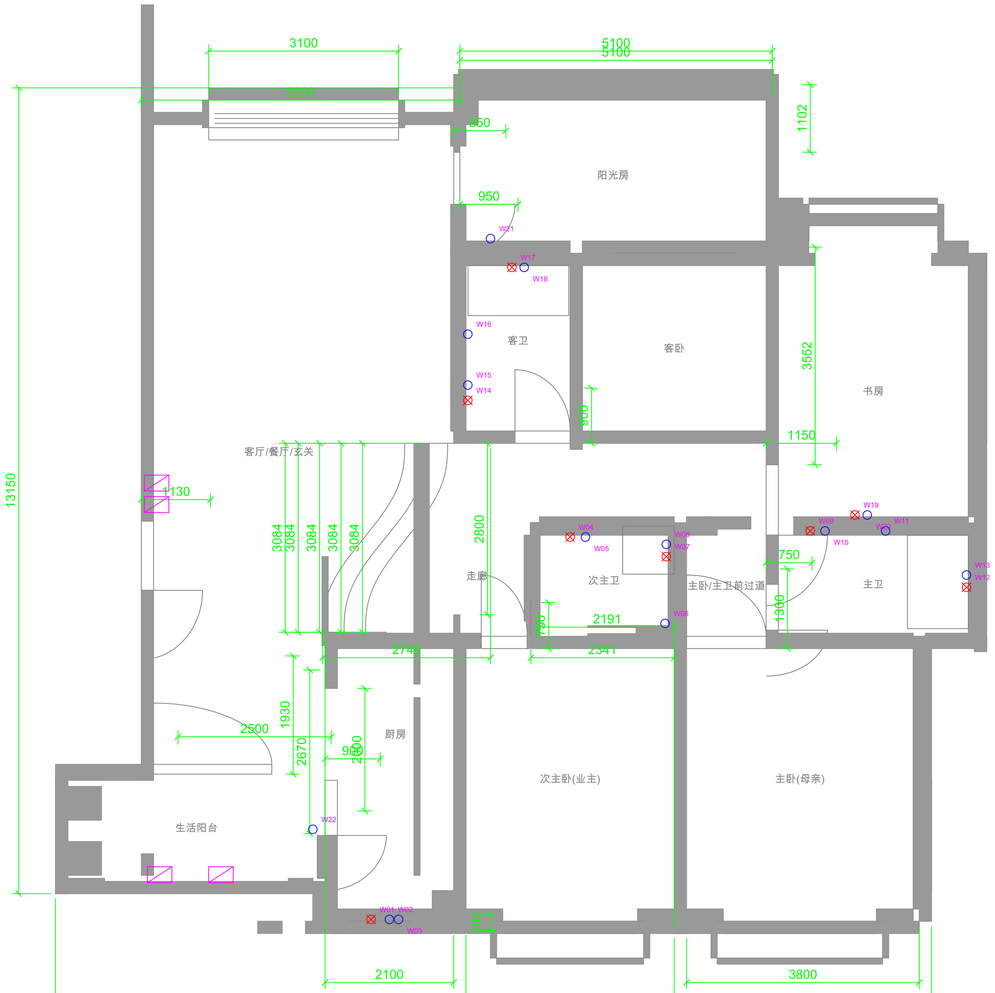


A303 给水点位示意 (冷热水) 1:50 CD_V01 PROPOSED / TBD

A303 给水点位 (CD_V01, 示意)

1. 只表达冷热水用水点; 排水由业主自行处理 -> OUT_OF_SCOPE / SITE_VERIFY_REQUIRED
2. 点位按模型洁具定位; H 为出水口距本层完成地面; 全部 PROPOSED
3. 给水入户、水表、总阀、热水器位置 TBD; 热水器假定在生活阳台
4. 管材、管径、热水循环、减压与防结露由施工方深化
5. 卫浴墙面不开槽: 出水点下引方式 TBD (假墙/包管/台盆柜内)
6. ○ 冷水 ⊗ 热水 灰框 = 淋浴区 (模型托盘/玻璃)

A303 给水点位 (冷热水, 示意, PROPOSED

图号 A303 比例 1:50 图幅 A1 单位 mm

状态: 初步设计 PRELIMINARY_DESIGN - 非正式施工图, 尺寸须现场复核

源: A303_给水点位.dxf sha256:20c58d0430

出图: publish_dxf.py 2026-11-01